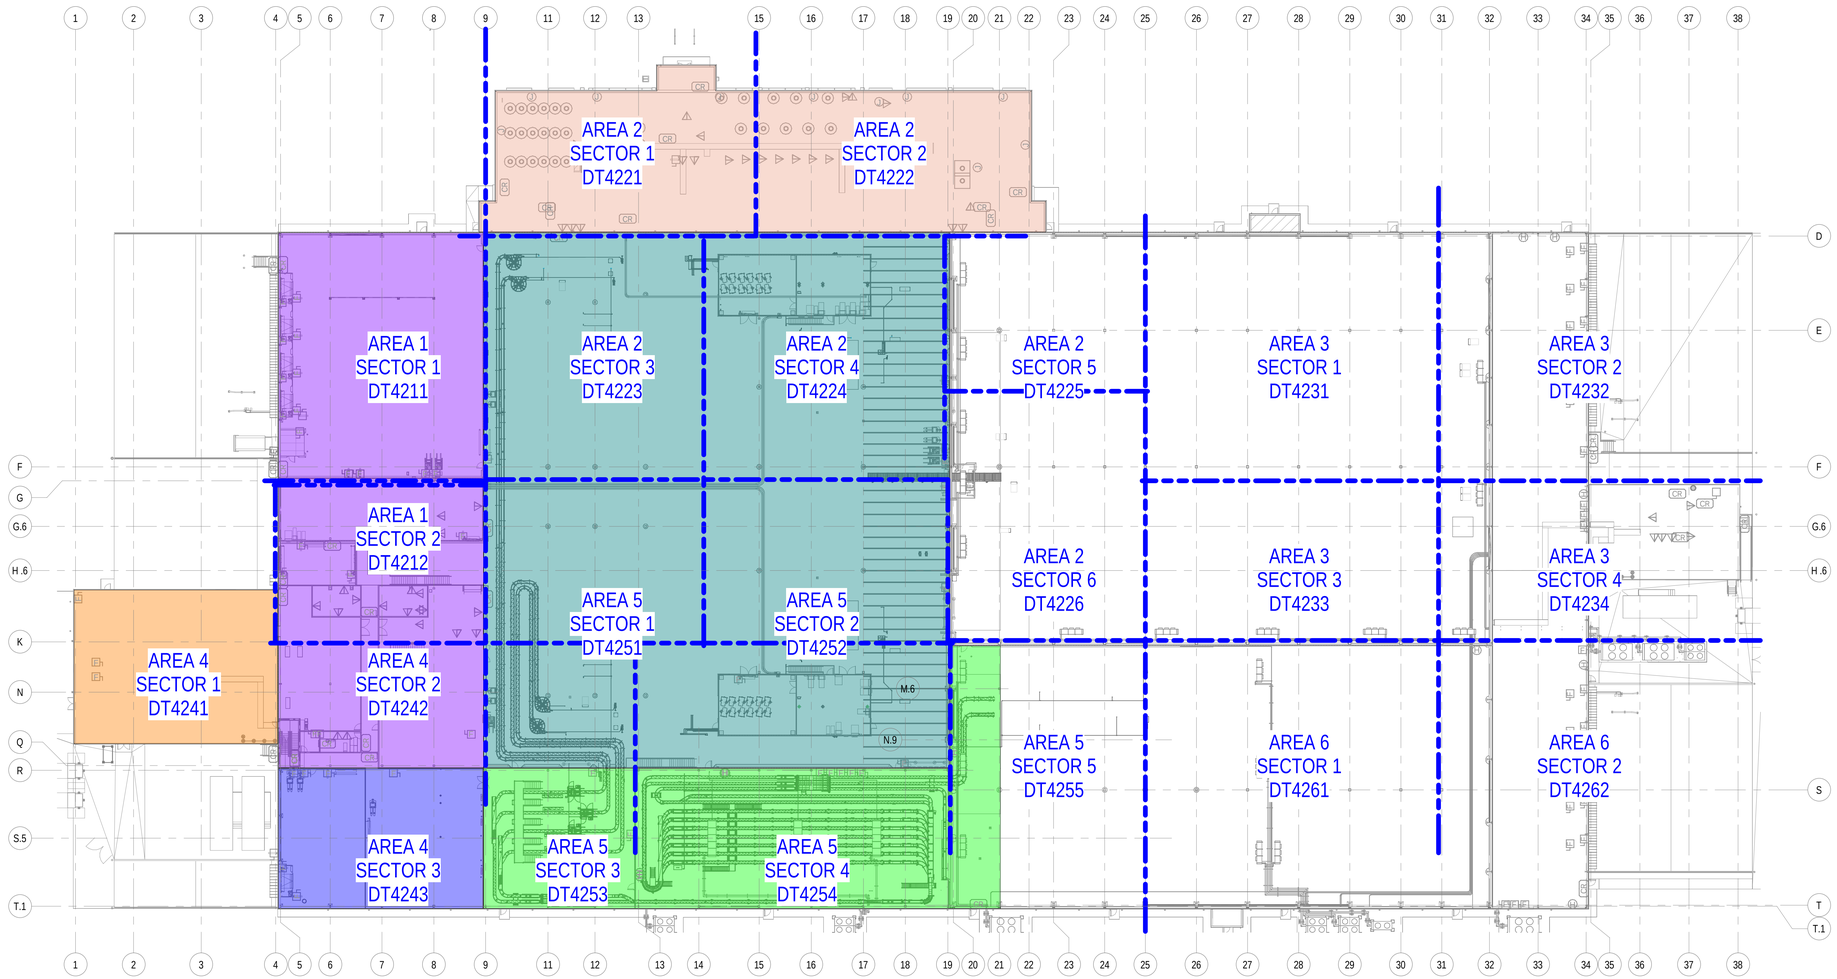

A1 PROCESS TELECOM OVERALL 2ND FLOOR PLAN

SCALE: 1" = 30'-0"

0' 15' 30' 60' 90'

FUNCTIONAL AREA LEGEND

- 10 - NEST RUN
- 20 - EGG PROCESSING
- 30 - PROCESS ANCILLARY
- 40 - FINISHED GOODS
- 50 - PALLET WASHING
- 60 - UTILITIES
- 70 - ADMIN

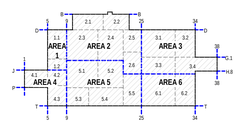

KEY PLAN

SECTORS

N

OWNER

EST. 2007 Vital FARMS®

PROJECT INFORMATION

VITAL FARMS
EGG CENTRAL 2
SEYMOUR,IN

stellar
TAKING SOLUTIONS FURTHER

OPERATING AS:
THE STELLAR GROUP
2900 HARTLEY ROAD, JACKSONVILLE, FL, 32257 (904) 260-2900
WWW.STELLAR.NET

SEAL

Professional certification. I hereby certify that these documents were prepared or approved by me, and that I am a duly licensed professional architect/engineer under the laws of the state of IN .

CONSULTANT

The Stellar Group, Inc.
All rights reserved. No part of this work may be used, reproduced, distributed, displayed, or otherwise communicated in any form or by any means without the prior written consent of The Stellar Group, Inc.

REVISIONS

NO.	DESCRIPTION	DATE
A	DESIGN DEVELOPMENT 2	12/12/2025
B	ISSUED FOR BID	01/16/2026
C	REVISED FOR BID	02/06/2026
D	GMP ISSUE	04/02/2026

DATE ISSUED:	12/12/2025
DESIGNED BY:	KDK
REVIEWED BY:	MAM
A/E/OR:	
PROJECT NUMBER:	07645

SHEET TITLE

PROCESS TELECOM OVERALL 2ND FLOOR PLAN

SHEET ID

DT1201

PRINT IN COLOR

4/3/2026 1:21:32 AM Autodesk Docs://07645_Vital Farms Egg Central Station 2/07645_VF EGG STA 2_D_R23.rvt