CARD READER EQUIPMENT ID'S REVISED.
3 MORE CARD READERS ADDED.

ACCESS CONTROL CONNECTION SCHEDULE

EQUIPMENT ID	EQUIPMENT DESCRIPTION	FED FROM
CR-AC-2401A	CARD READER	ACP-3001_17
CR-AC-2404B	CARD READER	ACP-3001_15
CR-AC-2406A	CARD READER - IT ROOM	ACP-3001_7
CR-AC-2410B	CARD READER	ACP-3001_16
Grand total: 4		

NOTES

1. ALL NETWORK DROPS SHALL BE TAGGED ON BOTH ENDS OF CABLE WITH "FROM / TO" FORMAT WITH BRADY B-427 ROTATING VINYL WIRE LABELS. (EX. 2001T-SW01_24 / TD-1001)

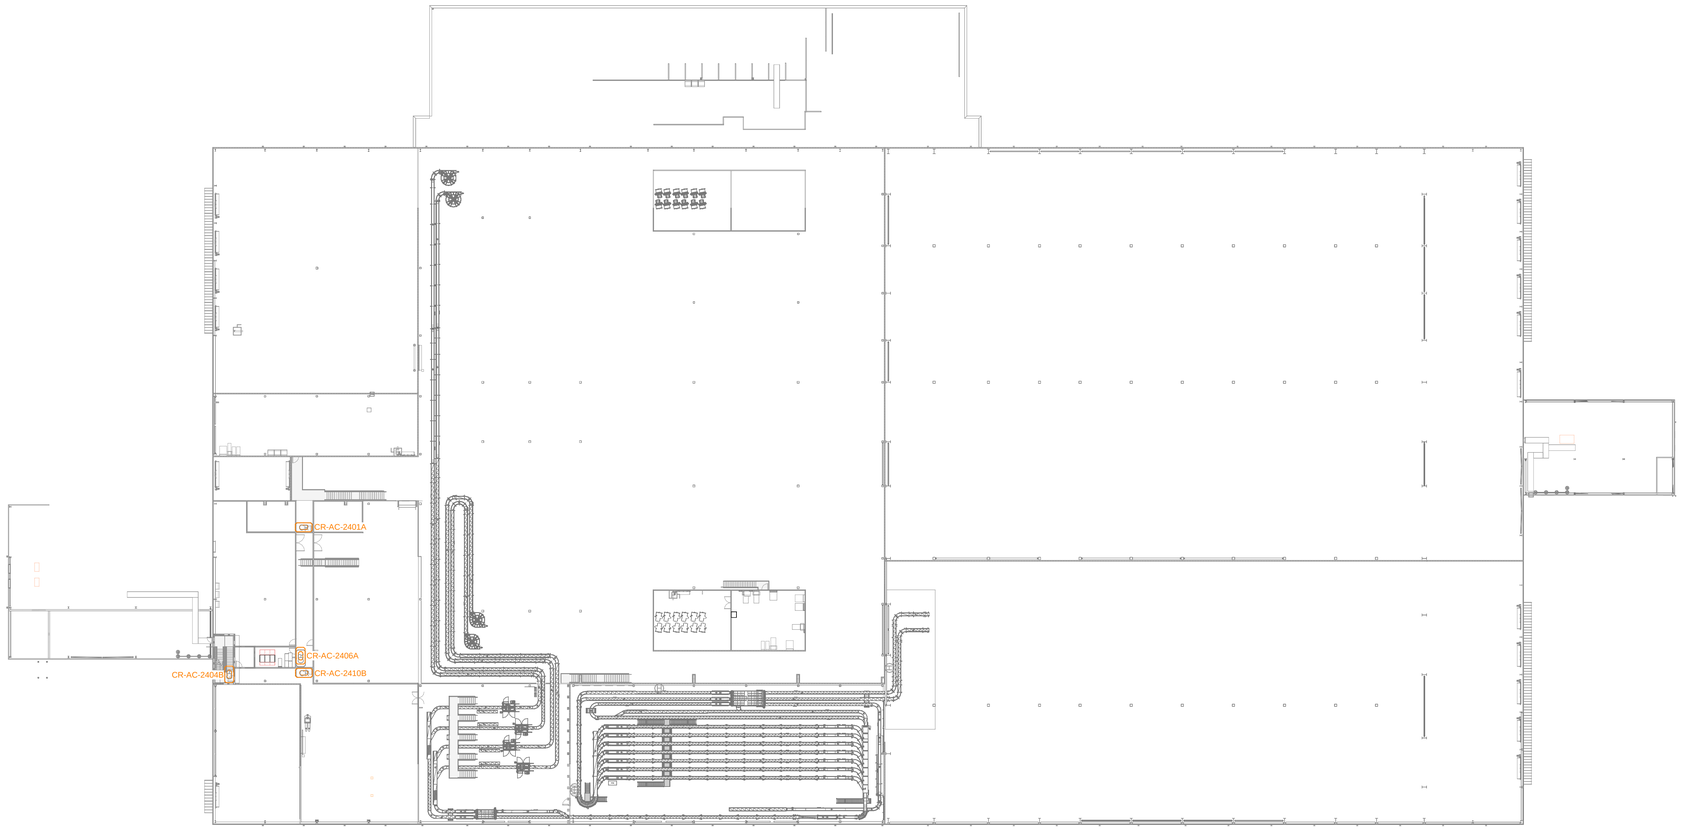

A1 OVERALL 2ND FLOOR ACCESS CONTROL LOCATIONS

SCALE: 1" = 30'-0"

0' 15' 30' 60' 90'

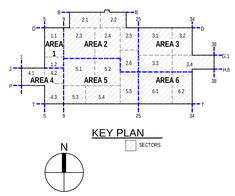

KEY PLAN

SECTORS

OWNER

PROJECT INFORMATION

VITAL FARMS
EGG CENTRAL 2
SEYMOUR,IN

stellar
TAKING SOLUTIONS FURTHER

OPERATING AS:
THE STELLAR GROUP
2900 HARTLEY ROAD, JACKSONVILLE, FL, 32257 (904) 260-2900
WWW.STELLAR.NET

SEAL

Professional certification. I hereby certify that these documents were prepared or approved by me, and that I am a duly licensed professional architect/engineer under the laws of the state of IN.

CONSULTANT

The Stellar Group, Inc.
All rights reserved. No part of this work may be used, reproduced, distributed, displayed, or otherwise communicated in any form or by any means without the prior written consent of The Stellar Group, Inc.

REVISIONS

NO.	DESCRIPTION	DATE
A	DESIGN DEVELOPMENT 2	12/12/2025
B	ISSUED FOR BID	01/16/2026
C	REVISED FOR BID	02/06/2026
D	GMP ISSUE	04/02/2026

DATE ISSUED:	12/12/2025
DESIGNED BY:	ARS
REVIEWED BY:	CDS
A/EOR:	
PROJECT NUMBER:	07645

SHEET TITLE

PROCESS TELECOM OVERALL 2ND FLOOR ACCESS CONTROL LOCATIONS

SHEET ID

DT1213

PRINT IN COLOR

4/3/2026 1:46:15 AM Autodesk Docs://07645_Vital Farms Egg Central Station 2/07645_VF EGG STA 2_D_R23.rvt