TELECOMM / DATA CONNECTION SCHEDULE

EQUIPMENT ID	EQUIPMENT DESCRIPTION	IDF	SWITCH / PORT
PNL30002	WALCHEM I-9 CONTROLLER	2I01	2I01OT-SW01_1
TD-3001	TWO (2) RJ45 DATA JACKS	2I01	2I01IT-SW01_16
TD-3002	TWO (2) RJ45 DATA JACKS	2I01	2I01IT-SW01_17
TD-3003	TWO (2) RJ45 DATA JACKS	2I01	2I01IT-SW01_19
CAM-3006	CAMERA	2M21	2M21CS-SW01_9
CAM-3007	CAMERA	2M21	2M21CS-SW01_10

Grand total: 6

ACCESS CONTROL CONNECTION SCHEDULE

EQUIPMENT ID	EQUIPMENT DESCRIPTION	FED FROM
CR-AC-1102A	CARD READER	ACP-3001_3
CR-AC-1103A	CARD READER	ACP-3001_4
CR-AC-1105A	CARD READER	ACP-3001_13
CR-BO-1106A	EMPLOYEE BADGE OUT	ACP-3001_11

Grand total: 4

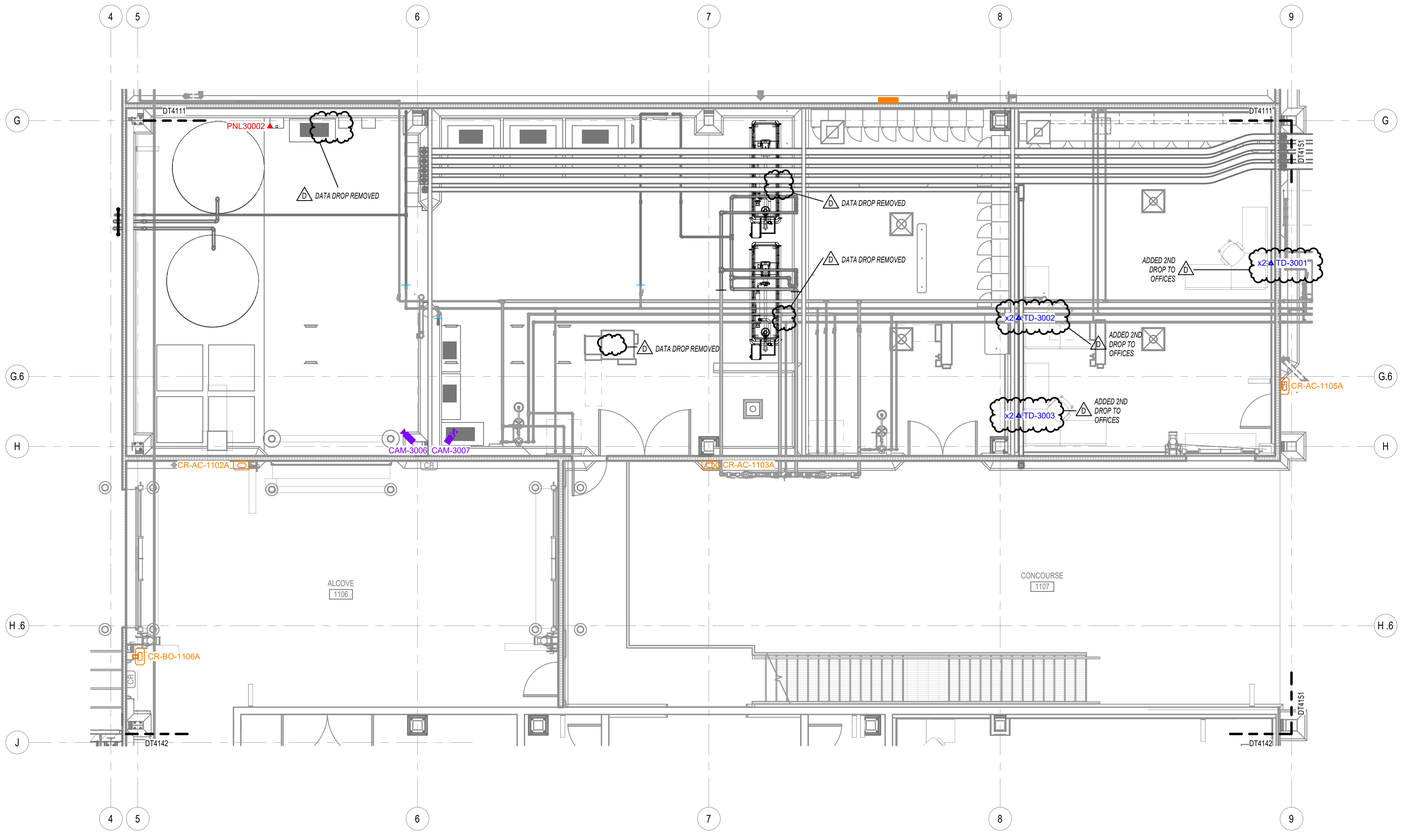

A1 ENLARGED PROCESS TELECOM 1ST FLOOR PLAN, AREA 1 SECTOR 2

SCALE: 3/16" = 1'-0"

0' 4' 8' 12' 16'

NOTES

1. ALL NETWORK DROPS SHALL BE TAGGED ON BOTH ENDS OF CABLE WITH "FROM / TO" FORMAT WITH BRADY B-427 ROTATING VINYL WIRE LABELS. (EX. 2I01IT-SW01_24 / TD-1001)
2. DATA DROPS MARKED WITH x2 SHALL BE DESIGNATED A / B TOP TO BOTTOM

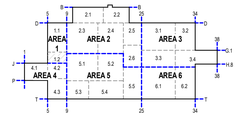

KEY PLAN

SECTORS

N

OWNER

PROJECT INFORMATION

VITAL FARMS
EGG CENTRAL 2
SEYMOUR,IN

stellar
TAKING SOLUTIONS FURTHER

OPERATING AS:
THE STELLAR GROUP
2900 HARTLEY ROAD, JACKSONVILLE, FL. 32257 (904) 260-2900
WWW.STELLAR.NET

SEAL

Professional certification. I hereby certify that these documents were prepared or approved by me, and that I am a duly licensed professional architect/engineer under the laws of the state of IN .

CONSULTANT

The Stellar Group, Inc.
All rights reserved. No part of this work may be used, reproduced, distributed, displayed, or otherwise communicated in any form or by any means without the prior written consent of The Stellar Group, Inc.

REVISIONS

NO.	DESCRIPTION	DATE
A	DESIGN DEVELOPMENT 2	12/12/2025
B	ISSUED FOR BID	01/16/2026
C	REVISED FOR BID	02/06/2026
D	GMP ISSUE	04/02/2026

DATE ISSUED:	12/12/2025
DESIGNED BY:	EJT
REVIEWED BY:	MAM
A/EOR:	
PROJECT NUMBER:	07645

SHEET TITLE

PROCESS TELECOM 1ST FLOOR PLAN, AREA 1 SECTOR 2

SHEET ID

DT4112

PRINT IN COLOR

4/3/2026 2:08:06 AM Autodesk Docs://07645_Vital Farms Egg Central Station 2/07645_VF EGG STA 2_D_R23.rvt