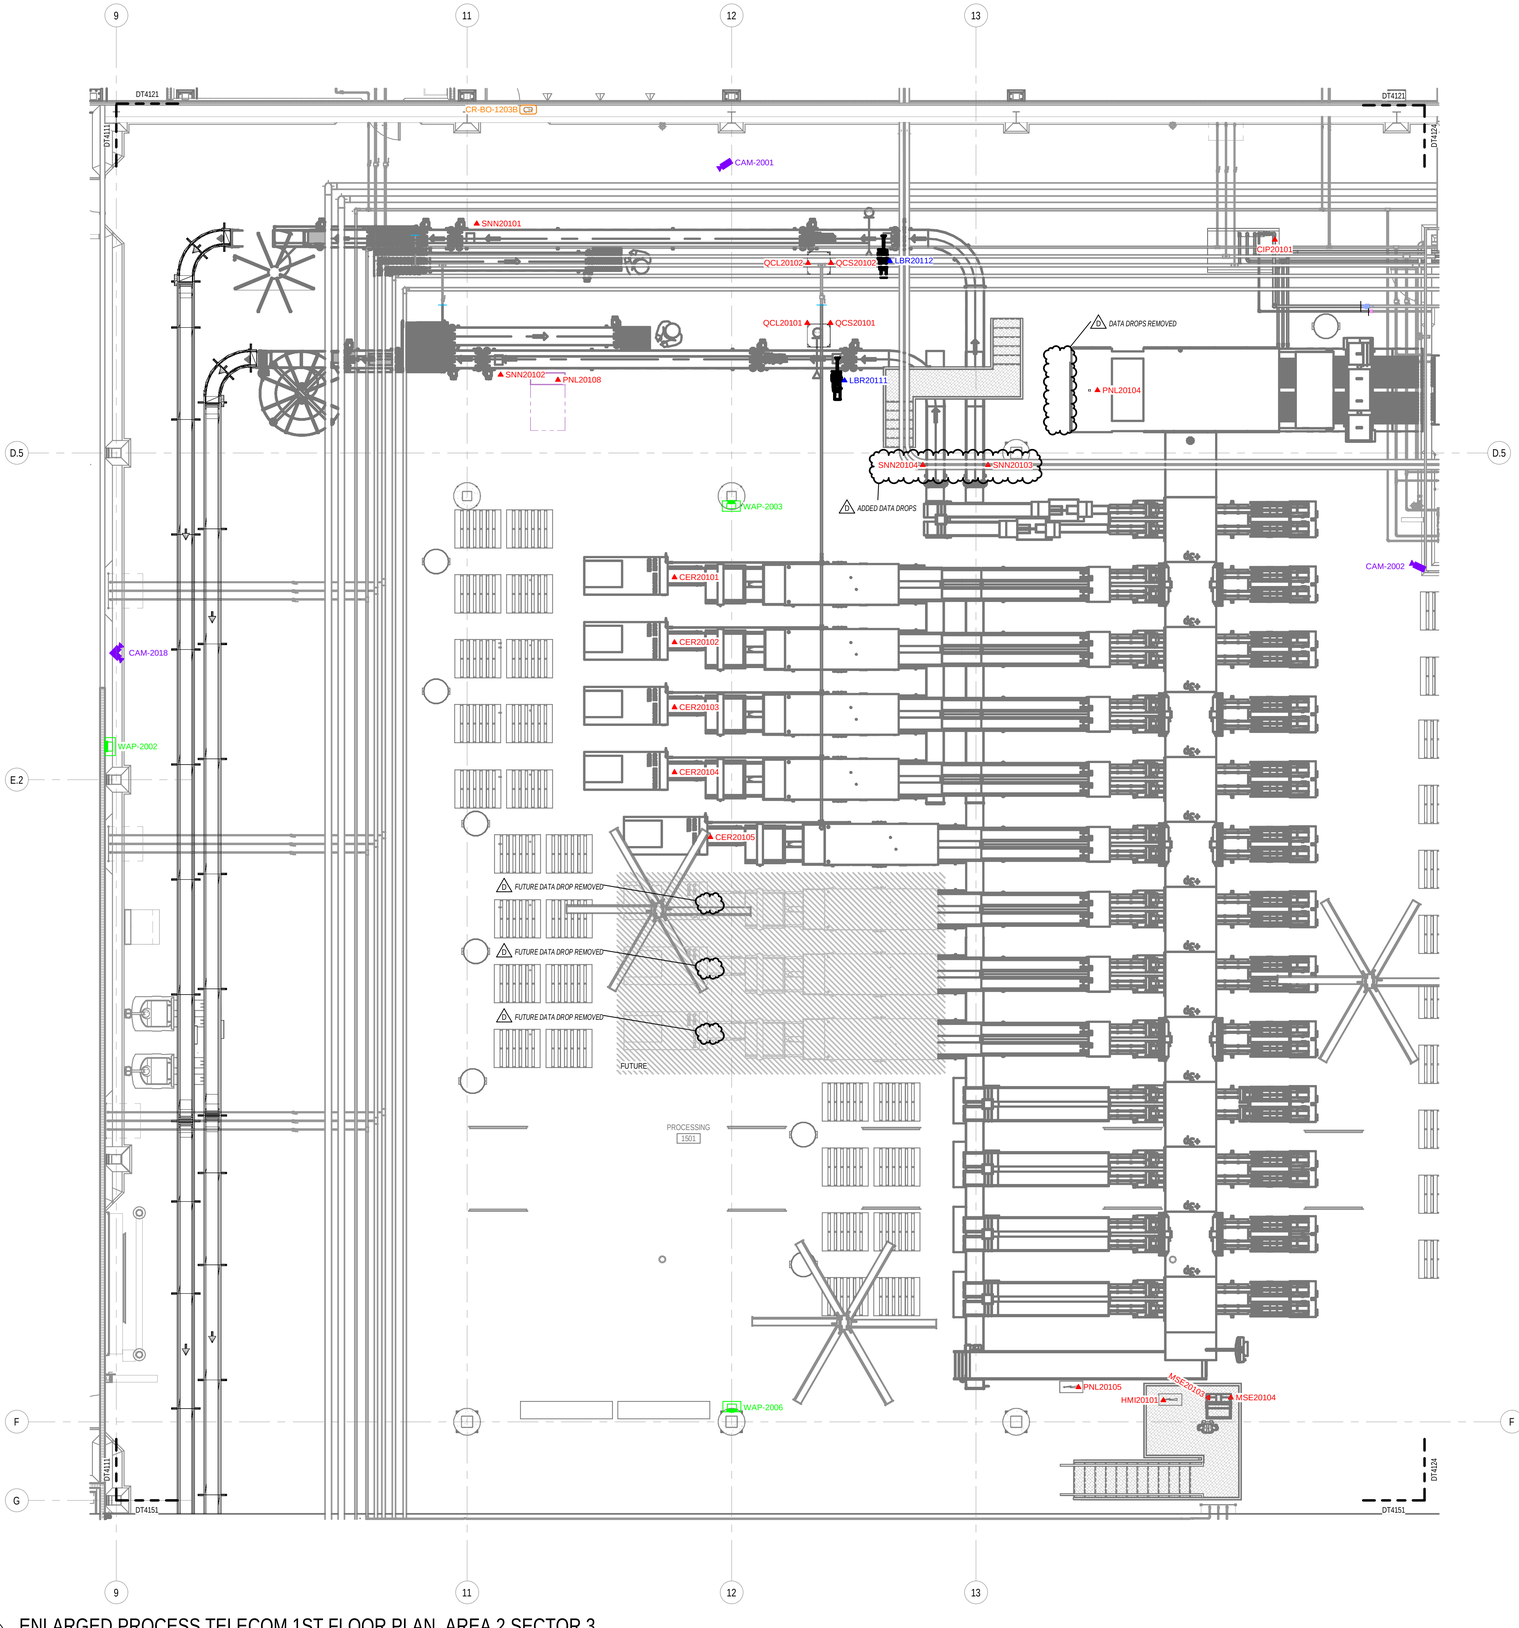

A1 ENLARGED PROCESS TELECOM 1ST FLOOR PLAN, AREA 2 SECTOR 3

SCALE: 3/16" = 1'-0"

0' 4' 8' 12' 16'

TELECOMM / DATA CONNECTION SCHEDULE

EQUIPMENT ID	EQUIPMENT DESCRIPTION	IDF	SWITCH / PORT
CAM-2001	CAMERA	202	202CS-SW01_1
CAM-2002	CAMERA	202	202CS-SW01_2
CAM-2018	DUAL CAMERA	202	202CS-SW01_6
CER20101	CASE ERECTOR	202	2020T-SW01_11
CER20102	CASE ERECTOR	202	2020T-SW01_12
CER20103	CASE ERECTOR	202	2020T-SW01_13
CER20104	CASE ERECTOR	202	2020T-SW01_14
CER20105	CASE ERECTOR	202	2020T-SW01_15
CIP20101	EGG GRADER CIP	202	2020T-SW01_28
HMI20101	SCADA HMI	202	2020T-SW01_33
LBR20111	PRINT APPLY LABELER	202	2020T-SW01_8
LBR20112	PRINT APPLY LABELER	202	2020T-SW01_9
MSE20103	OPERATOR STATION	202	2020T-SW01_18
MSE20104	OVOTRACK PC STATION	202	2020T-SW01_19
PNL20104	EGG GRADER CONTROL PANEL	202	2020T-SW01_5
PNL20105	CASE PACK TAKEAWAY CONTROL PANEL	202	2020T-SW01_6
PNL20108	QC CONVEYOR PANEL	202	2020T-SW01_7
QCL20101	QC CHECK / LAB	202	2020T-SW01_24
QCL20102	QC CHECK / LAB	202	2020T-SW01_25
QCS20101	QC ONLINE WORKSTATION	202	2020T-SW01_22
QCS20102	QC ONLINE WORKSTATION	202	2020T-SW01_23
SNN20101	OVOTRACK FIXED CASE SCANNER	202	2020T-SW01_26
SNN20102	OVOTRACK FIXED CASE SCANNER	202	2020T-SW01_27
SNN20103	OVOTRACK FIXED CASE SCANNER	202	2020T-SW01_31
SNN20104	OVOTRACK FIXED CASE SCANNER	202	2020T-SW01_32
WAP-2002	WIRELESS ACCESS POINT	202	202T-SW01_2
WAP-2003	WIRELESS ACCESS POINT	202	202T-SW01_3
WAP-2006	WIRELESS ACCESS POINT	202	202T-SW01_6

Grand total: 28

ACCESS CONTROL CONNECTION SCHEDULE

EQUIPMENT ID	EQUIPMENT DESCRIPTION	FED FROM
CR-BO-1203B	EMPLOYEE BADGE OUT	ACP-7001_7

Grand total: 1

NOTES

1. ALL NETWORK DROPS SHALL BE TAGGED ON BOTH ENDS OF CABLE WITH "FROM / TO" FORMAT WITH BRADY B-427 ROTATING VINYL WIRE LABELS. (EX. 2001IT-SW01_24 / TD-1001)

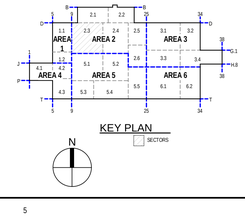

OWNER

PROJECT INFORMATION

VITAL FARMS
EGG CENTRAL 2
SEYMOUR,IN

OPERATING AS:
THE STELLAR GROUP
2900 HARTLEY ROAD, JACKSONVILLE, FL, 32257 (904) 260-2900
WWW.STELLAR.NET

SEAL

Professional certification. I hereby certify that these documents were prepared or approved by me, and that I am a duly licensed professional architect/engineer under the laws of the state of IN.

CONSULTANT

The Stellar Group, Inc.
All rights reserved. No part of this work may be used, reproduced, distributed, displayed, or otherwise communicated in any form or by any means without the prior written consent of The Stellar Group, Inc.

REVISIONS

NO.	DESCRIPTION	DATE
A	DESIGN DEVELOPMENT 2	12/12/2025
B	ISSUED FOR BID	01/16/2026
C	REVISED FOR BID	02/06/2026
D	GMP ISSUE	04/02/2026

DATE ISSUED:	12/12/2025
DESIGNED BY:	EJT
REVIEWED BY:	MAM
A/EOR:	
PROJECT NUMBER:	07645

SHEET TITLE

PROCESS TELECOM 1ST FLOOR PLAN, AREA 2 SECTOR 3

SHEET ID

DT4123

PRINT IN COLOR

4/3/2026 1:08:05 AM Autodesk Docs://07645_Vital Farms Egg Central Station 2/07645_VF EGG STA 2_D_R23.rvt