TELECOMM / DATA CONNECTION SCHEDULE

EQUIPMENT ID	EQUIPMENT DESCRIPTION	IDF	SWITCH / PORT
PNL10008	VERTICAL CONVEYOR PANEL	2I04	2I04OT-SW01_2
CAM-1002	CAMERA	2I05	2I05CS-SW01_1
MSE10105	OVOTRACK PC STATION WITH PRINTER	2I05	2I05OT-SW01_1
PNL10006	VERTICAL CONVEYOR PANEL	2I05	2I05OT-SW01_12
SNN10106	OVOTRACK PALLET SCAN STATION	2I05	2I05OT-SW01_3
SNN10107	OVOTRACK PALLET SCAN STATION	2I05	2I05OT-SW01_18
WAP-1005	WIRELESS ACCESS POINT	2I05	2I05IT-SW01_1

Grand total: 7

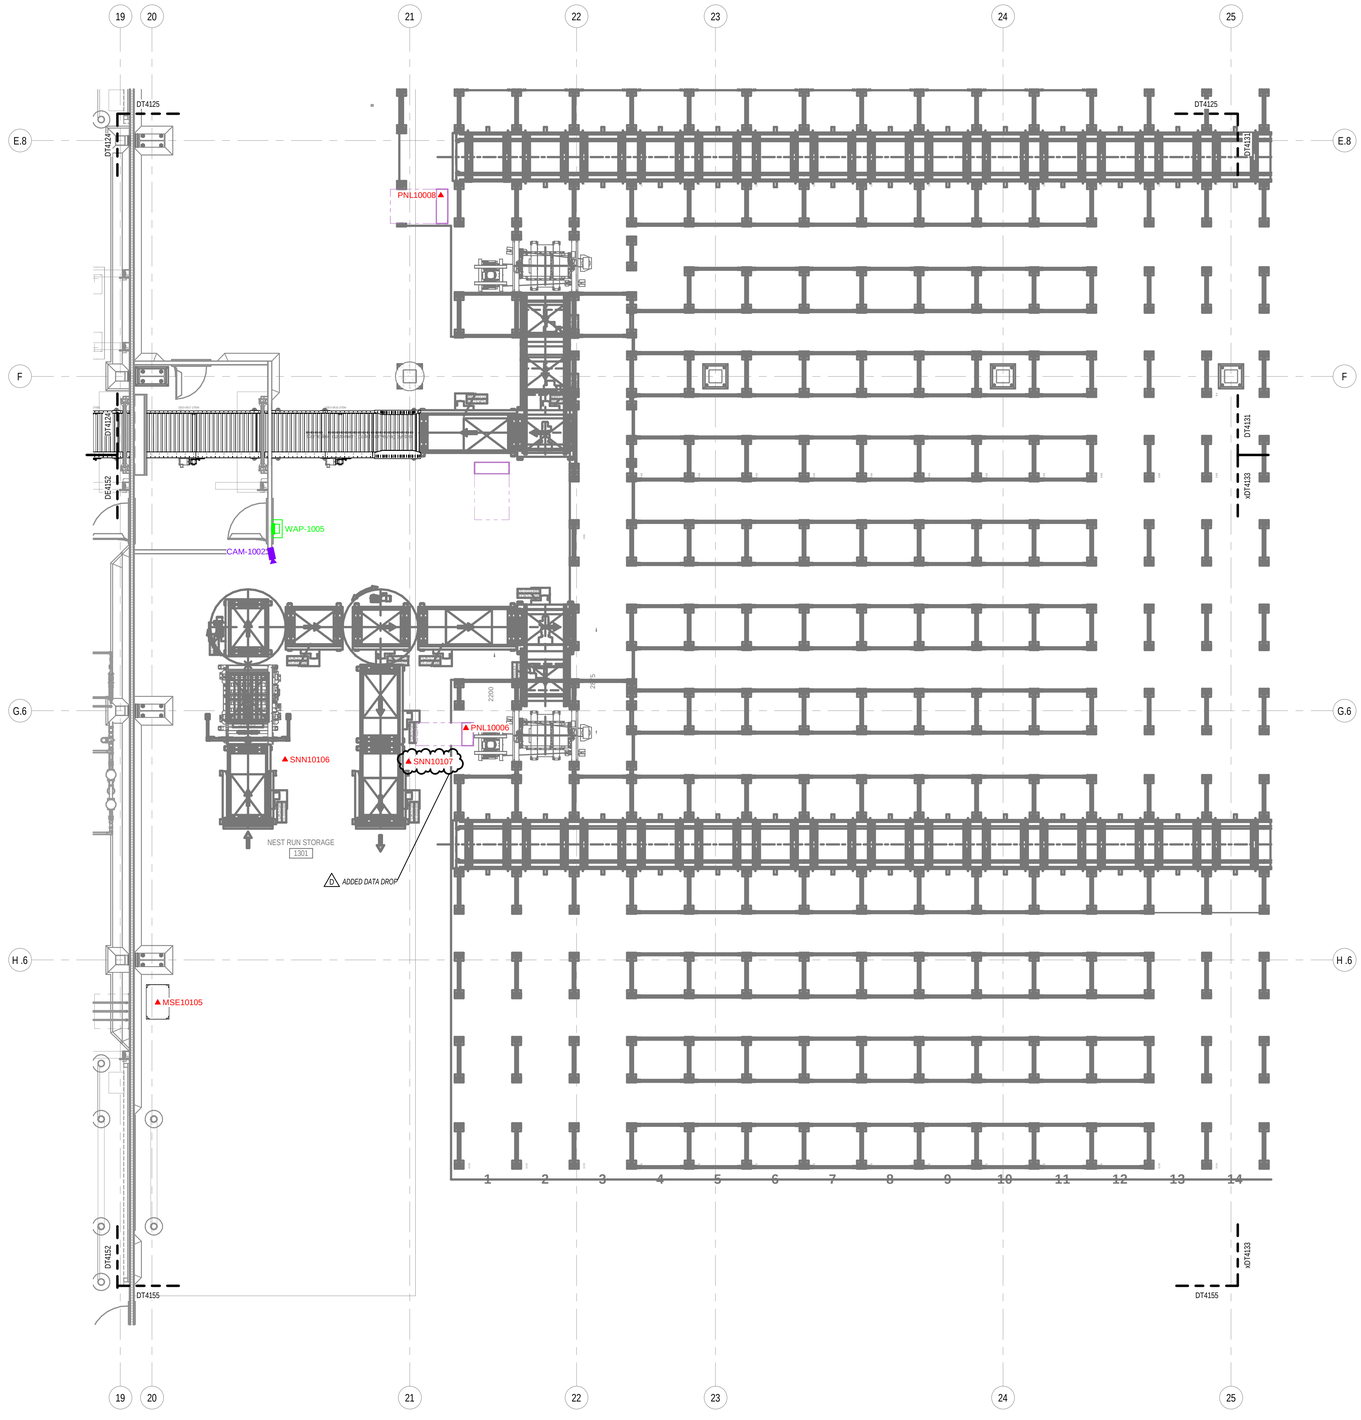

A1 ENLARGED PROCESS TELECOM 1ST FLOOR PLAN, AREA 2 SECTOR 6

SCALE: 3/16" = 1'-0"

0' 4' 8' 12' 16'

NOTES

1. ALL NETWORK DROPS SHALL BE TAGGED ON BOTH ENDS OF CABLE WITH "FROM / TO" FORMAT WITH BRADY B-427 ROTATING VINYL WIRE LABELS. (EX. 2I01IT-SW01_24 / TD-1001)

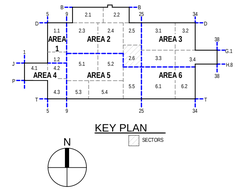

KEY PLAN

SECTORS

OWNER

PROJECT INFORMATION

VITAL FARMS
EGG CENTRAL 2
SEYMOUR,IN

OPERATING AS:
THE STELLAR GROUP
2900 HARTLEY ROAD, JACKSONVILLE, FL, 32257 (904) 260-2900
WWW.STELLAR.NET

SEAL

Professional certification. I hereby certify that these documents were prepared or approved by me, and that I am a duly licensed professional architect/engineer under the laws of the state of IN.

CONSULTANT

The Stellar Group, Inc.
All rights reserved. No part of this work may be used, reproduced, distributed, displayed, or otherwise communicated in any form or by any means without the prior written consent of The Stellar Group, Inc.

REVISIONS

NO.	DESCRIPTION	DATE
A	DESIGN DEVELOPMENT 2	12/12/2025
B	ISSUED FOR BID	01/16/2026
C	REVISED FOR BID	02/06/2026
D	GMP ISSUE	04/02/2026

DATE ISSUED:	12/12/2025
DESIGNED BY:	EJT
REVIEWED BY:	MAM
A/E/OR:	
PROJECT NUMBER:	07645

SHEET TITLE

PROCESS TELECOM 1ST FLOOR PLAN, AREA 2 SECTOR 6

SHEET ID

DT4126

PRINT IN COLOR

4/3/2026 1:09:18 AM Autodesk Docs://07645_Vital Farms Egg Central Station 2/07645_VF EGG STA 2_D_R23.rvt