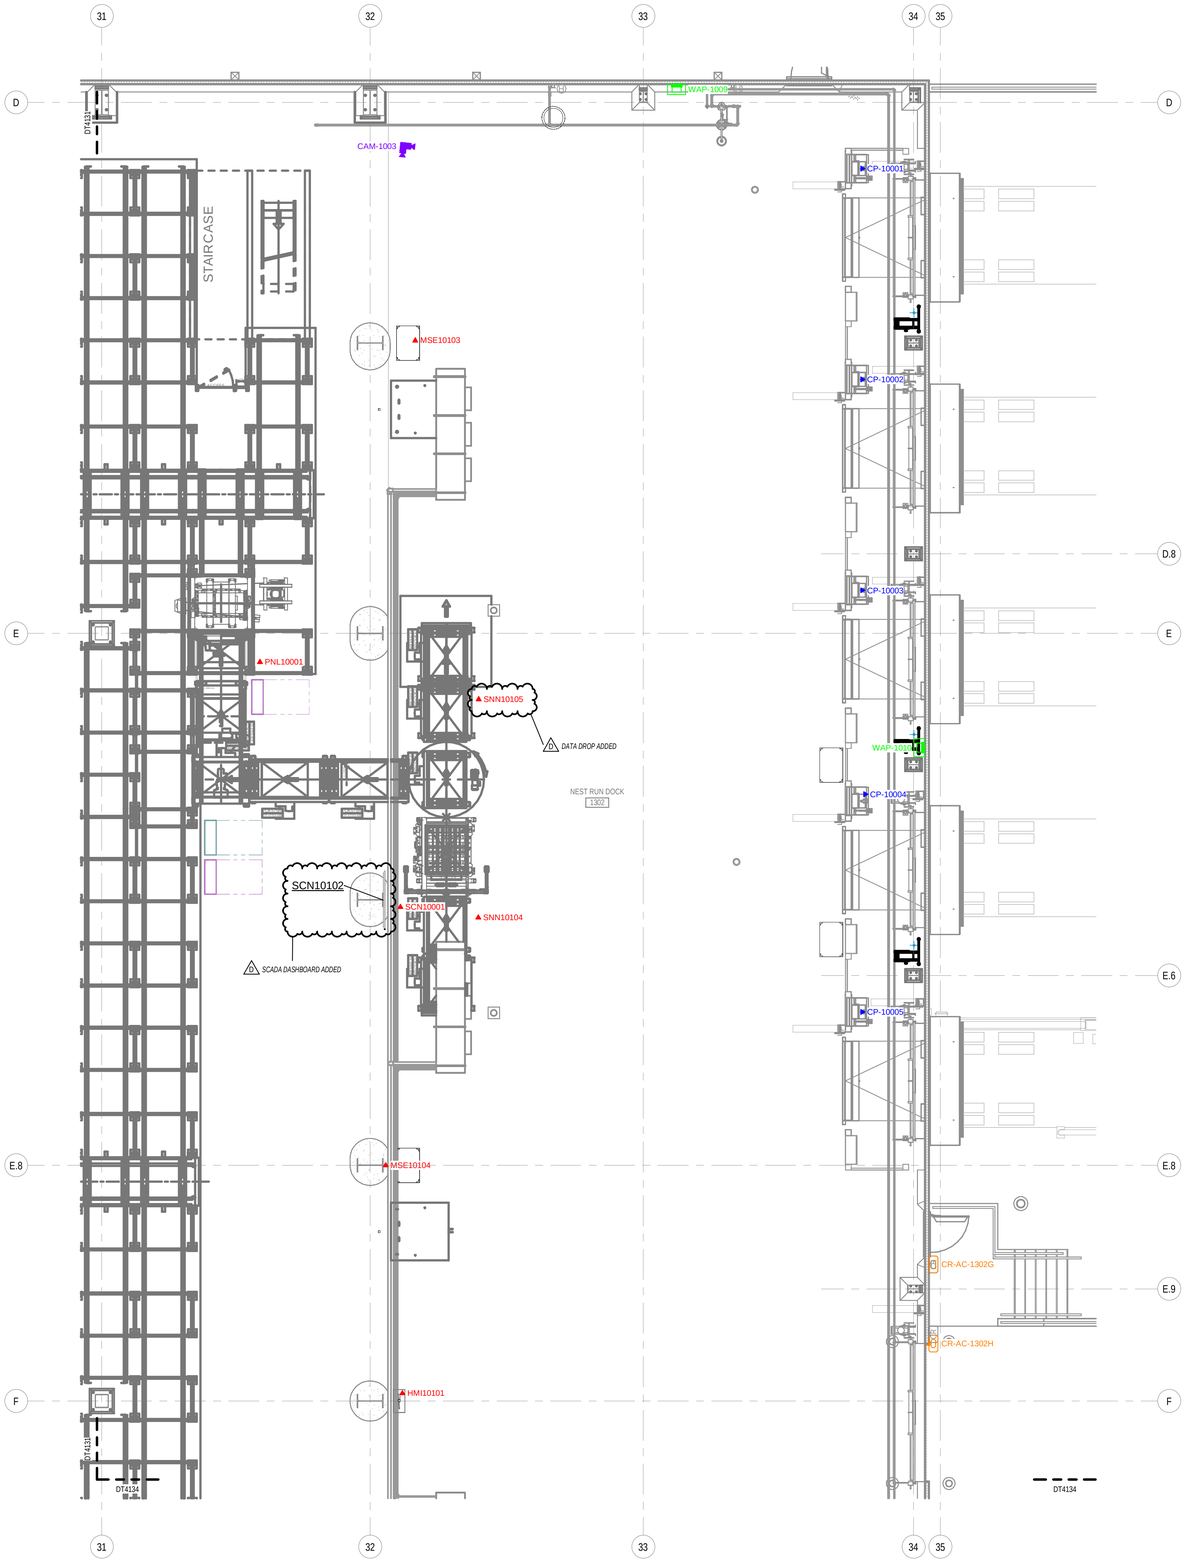

A1 ENLARGED PROCESS TELECOM 1ST FLOOR PLAN, AREA 3 SECTOR 2

SCALE: 3/16" = 1'-0"

0' 4' 8' 12' 16'

TELECOMM / DATA CONNECTION SCHEDULE

EQUIPMENT ID	EQUIPMENT DESCRIPTION	IDF	SWITCH / PORT
MSE10103	OVOTRACK PC STATION WITH PRINTER	2I04	2I04OT-SW01_3
PNL10001	VERTICAL CONVEYOR PANEL	2I04	2I04OT-SW01_1
SCN10001	OVOTRACK TV	2I04	2I04OT-SW01_4
CAM-1003	DUAL CAMERA	2I06	2I06CS-SW01_8
CP-10001	DOCK LEVELER CONTROL PANEL - RECEIVING DOCK 1302B	2I06	2I06IT-SW01_21
CP-10002	DOCK LEVELER CONTROL PANEL - RECEIVING DOCK 1302C	2I06	2I06IT-SW01_22
CP-10003	DOCK LEVELER CONTROL PANEL - RECEIVING DOCK 1302D	2I06	2I06IT-SW01_23
CP-10004	DOCK LEVELER CONTROL PANEL - RECEIVING DOCK 1302E	2I06	2I06IT-SW01_24
CP-10005	DOCK LEVELER CONTROL PANEL - RECEIVING DOCK 1302F	2I06	2I06IT-SW01_25
HMI10101	SCADA HMI	2I06	2I06OT-SW01_5
MSE10104	OVOTRACK PC STATION WITH PRINTER	2I06	2I06OT-SW01_1
SCN10102	SCADA DASHBOARD	2I06	2I06OT-SW01_15
SNN10104	OVOTRACK WEIGHSCALE SCAN STATION	2I06	2I06OT-SW01_2
SNN10105	OVOTRACK PALLET SCAN STATION	2I06	2I06OT-SW01_17
WAP-1009	WIRELESS ACCESS POINT	2I06	2I06IT-SW01_1
WAP-1010	WIRELESS ACCESS POINT	2I06	2I06IT-SW01_2

Grand total: 16

ACCESS CONTROL CONNECTION SCHEDULE

EQUIPMENT ID	EQUIPMENT DESCRIPTION	FED FROM
CR-AC-1302G	CARD READER	ACP-1001_1
CR-AC-1302H	CARD READER	ACP-1001_2

Grand total: 2

NOTES

1. ALL NETWORK DROPS SHALL BE TAGGED ON BOTH ENDS OF CABLE WITH "FROM / TO" FORMAT WITH BRADY B-427 ROTATING VINYL WIRE LABELS. (EX. 2I01IT-SW01_24 / TD-1001)

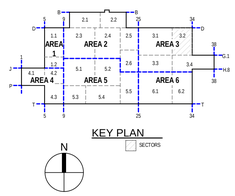

KEY PLAN

SECTORS

OWNER

PROJECT INFORMATION

VITAL FARMS
EGG CENTRAL 2
SEYMOUR,IN

OPERATING AS:
THE STELLAR GROUP
2900 HARTLEY ROAD, JACKSONVILLE, FL, 32257 (904) 260-2900
WWW.STELLAR.NET

SEAL

Professional certification. I hereby certify that these documents were prepared or approved by me, and that I am a duly licensed professional architect/engineer under the laws of the state of IN.

CONSULTANT

The Stellar Group, Inc.
All rights reserved. No part of this work may be used, reproduced, distributed, displayed, or otherwise communicated in any form or by any means without the prior written consent of The Stellar Group, Inc.

REVISIONS

NO.	DESCRIPTION	DATE
A	DESIGN DEVELOPMENT 2	12/12/2025
B	ISSUED FOR BID	01/16/2026
C	REVISED FOR BID	02/06/2026
D	GMP ISSUE	04/02/2026

DATE ISSUED: 12/12/2025
DESIGNED BY: EJT
REVIEWED BY: MAM
A/E/OR:
PROJECT NUMBER: 07645

SHEET TITLE

PROCESS TELECOM 1ST FLOOR PLAN, AREA 3 SECTOR 2

SHEET ID

DT4132

PRINT IN COLOR

4/3/2026 1:10:07 AM Autodesk Docs://07645_Vital Farms Egg Central Station 2/07645_VF EGG STA 2_D_R23.rvt