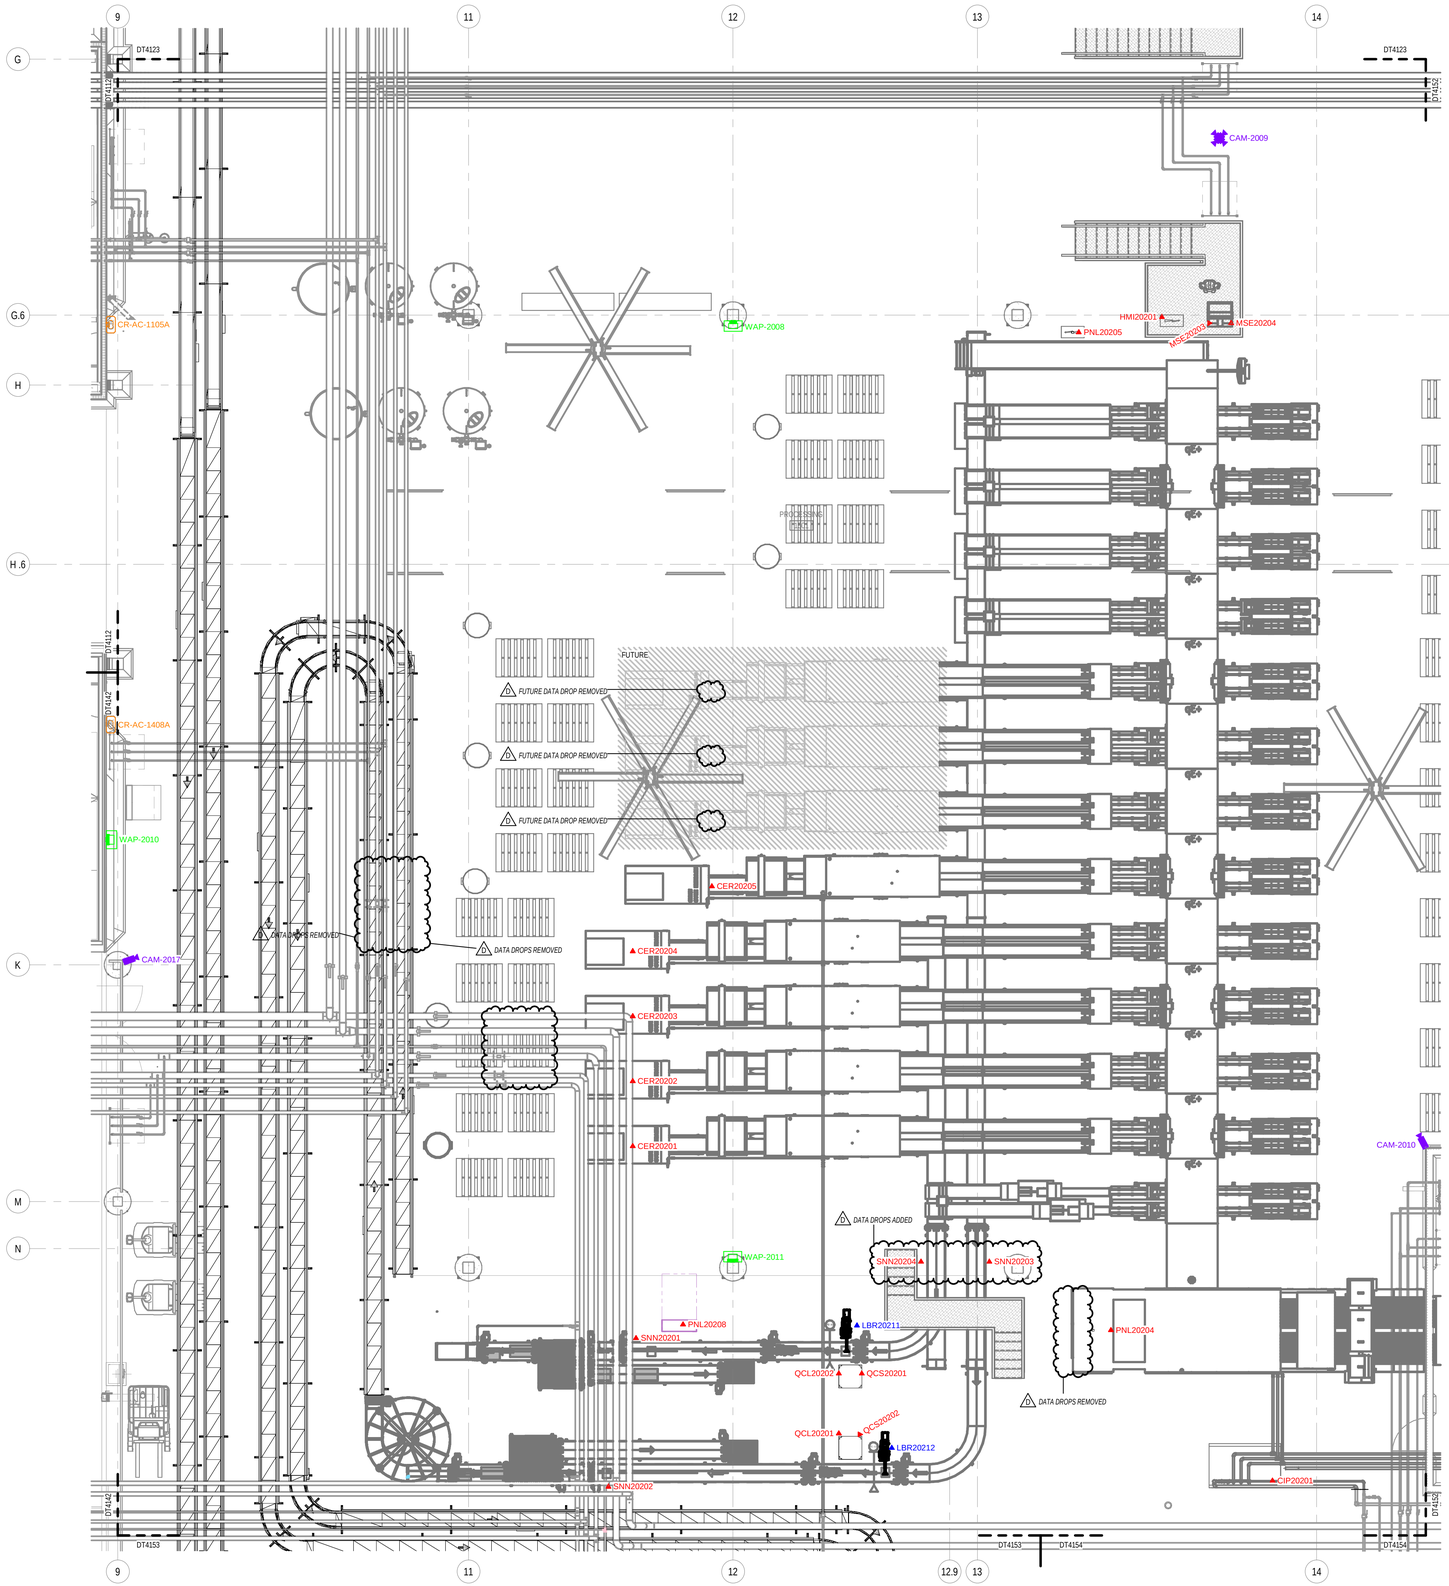

A1 ENLARGED PROCESS TELECOM 1ST FLOOR PLAN, AREA 5 SECTOR 1

SCALE: 3/16" = 1'-0"

0' 4' 8' 12' 16'

TELECOMM / DATA CONNECTION SCHEDULE

EQUIPMENT ID	EQUIPMENT DESCRIPTION	IDF	SWITCH / PORT
CAM-2009	QUAD CAMERA	2I03	2I03CS-SW01_1
CAM-2010	CAMERA	2I03	2I03CS-SW01_2
CAM-2017	CAMERA	2I03	2I03CS-SW01_8
CER20201	CASE ERECTOR	2I03	2I03OT-SW01_12
CER20202	CASE ERECTOR	2I03	2I03OT-SW01_13
CER20203	CASE ERECTOR	2I03	2I03OT-SW01_14
CER20204	CASE ERECTOR	2I03	2I03OT-SW01_15
CER20205	CASE ERECTOR	2I03	2I03OT-SW01_16
CIP20201	EGG GRADER CIP	2I03	2I03OT-SW01_27
HMI20201	SCADA HMI	2I03	2I03OT-SW02_8
LBR20211	PRINT APPLY LABELER	2I03	2I03IT-SW01_15
LBR20212	PRINT APPLY LABELER	2I03	2I03IT-SW01_16
MSE20203	OPERATOR STATION	2I03	2I03OT-SW01_19
MSE20204	OVOTRACK PC STATION	2I03	2I03OT-SW01_20
PNL20204	EGG GRADER CONTROL PANEL	2I03	2I03OT-SW01_2
PNL20205	CASE PACK TAKEAWAY CONTROL PANEL	2I03	2I03OT-SW01_3
PNL20208	QC CONVEYOR PANEL	2I03	2I03OT-SW01_5
QCL20201	QC CHECK / LAB	2I03	2I03OT-SW01_23
QCL20202	QC CHECK / LAB	2I03	2I03OT-SW01_24
QCS20201	QC ONLINE WORKSTATION	2I03	2I03OT-SW01_22
QCS20202	QC ONLINE WORKSTATION	2I03	2I03IT-SW01_17
SCN20103	SCADA DASHBOARD	2I03	2I03OT-SW02_7
SNN20201	OVOTRACK FIXED CASE SCANNER	2I03	2I03OT-SW01_25
SNN20202	OVOTRACK FIXED CASE SCANNER	2I03	2I03OT-SW01_26
SNN20203	OVOTRACK FIXED CASE SCANNER	2I03	2I03OT-SW02_9
SNN20204	OVOTRACK FIXED CASE SCANNER	2I03	2I03OT-SW02_10
WAP-2008	WIRELESS ACCESS POINT	2I03	2I03IT-SW01_1
WAP-2010	WIRELESS ACCESS POINT	2I03	2I03IT-SW01_3
WAP-2011	WIRELESS ACCESS POINT	2I03	2I03IT-SW01_4

Grand total: 29

ACCESS CONTROL CONNECTION SCHEDULE

EQUIPMENT ID	EQUIPMENT DESCRIPTION	FED FROM
CR-AC-1105A	CARD READER	ACP-3001_13
CR-AC-1408A	CARD READER	ACP-3001_10

Grand total: 2

NOTES

1. ALL NETWORK DROPS SHALL BE TAGGED ON BOTH ENDS OF CABLE WITH "FROM / TO" FORMAT WITH BRADY B-427 ROTATING VINYL WIRE LABELS. (EX. 2I01IT-SW01_24 / TD-1001)

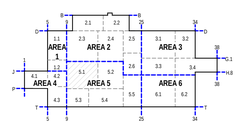

KEY PLAN

SECTORS

N

OWNER

PROJECT INFORMATION

VITAL FARMS EGG CENTRAL 2

SEYMOUR,IN

stellar TAKING SOLUTIONS FURTHER

OPERATING AS:
THE STELLAR GROUP
2900 HARTLEY ROAD, JACKSONVILLE, FL, 32257 (904) 260-2900
WWW.STELLAR.NET

SEAL

Professional certification. I hereby certify that these documents were prepared or approved by me, and that I am a duly licensed professional architect/engineer under the laws of the state of IN.

CONSULTANT

The Stellar Group, Inc.
All rights reserved. No part of this work may be used, reproduced, distributed, displayed, or otherwise communicated in any form or by any means without the prior written consent of The Stellar Group, Inc.

REVISIONS

NO.	DESCRIPTION	DATE
A	DESIGN DEVELOPMENT 2	12/12/2025
B	ISSUED FOR BID	01/16/2026
C	REVISED FOR BID	02/06/2026
D	GMP ISSUE	04/02/2026

DATE ISSUED:	12/12/2025
DESIGNED BY:	EJT
REVIEWED BY:	MAM
AIEOR:	
PROJECT NUMBER:	07645

SHEET TITLE

PROCESS TELECOM 1ST FLOOR PLAN, AREA 5 SECTOR 1

SHEET ID

DT4151

PRINT IN COLOR

4/3/2026 1:12:32 AM Autodesk Docs://07645_Vital Farms Egg Central Station 2/07645_VF EGG STA 2_D_R23.rvt