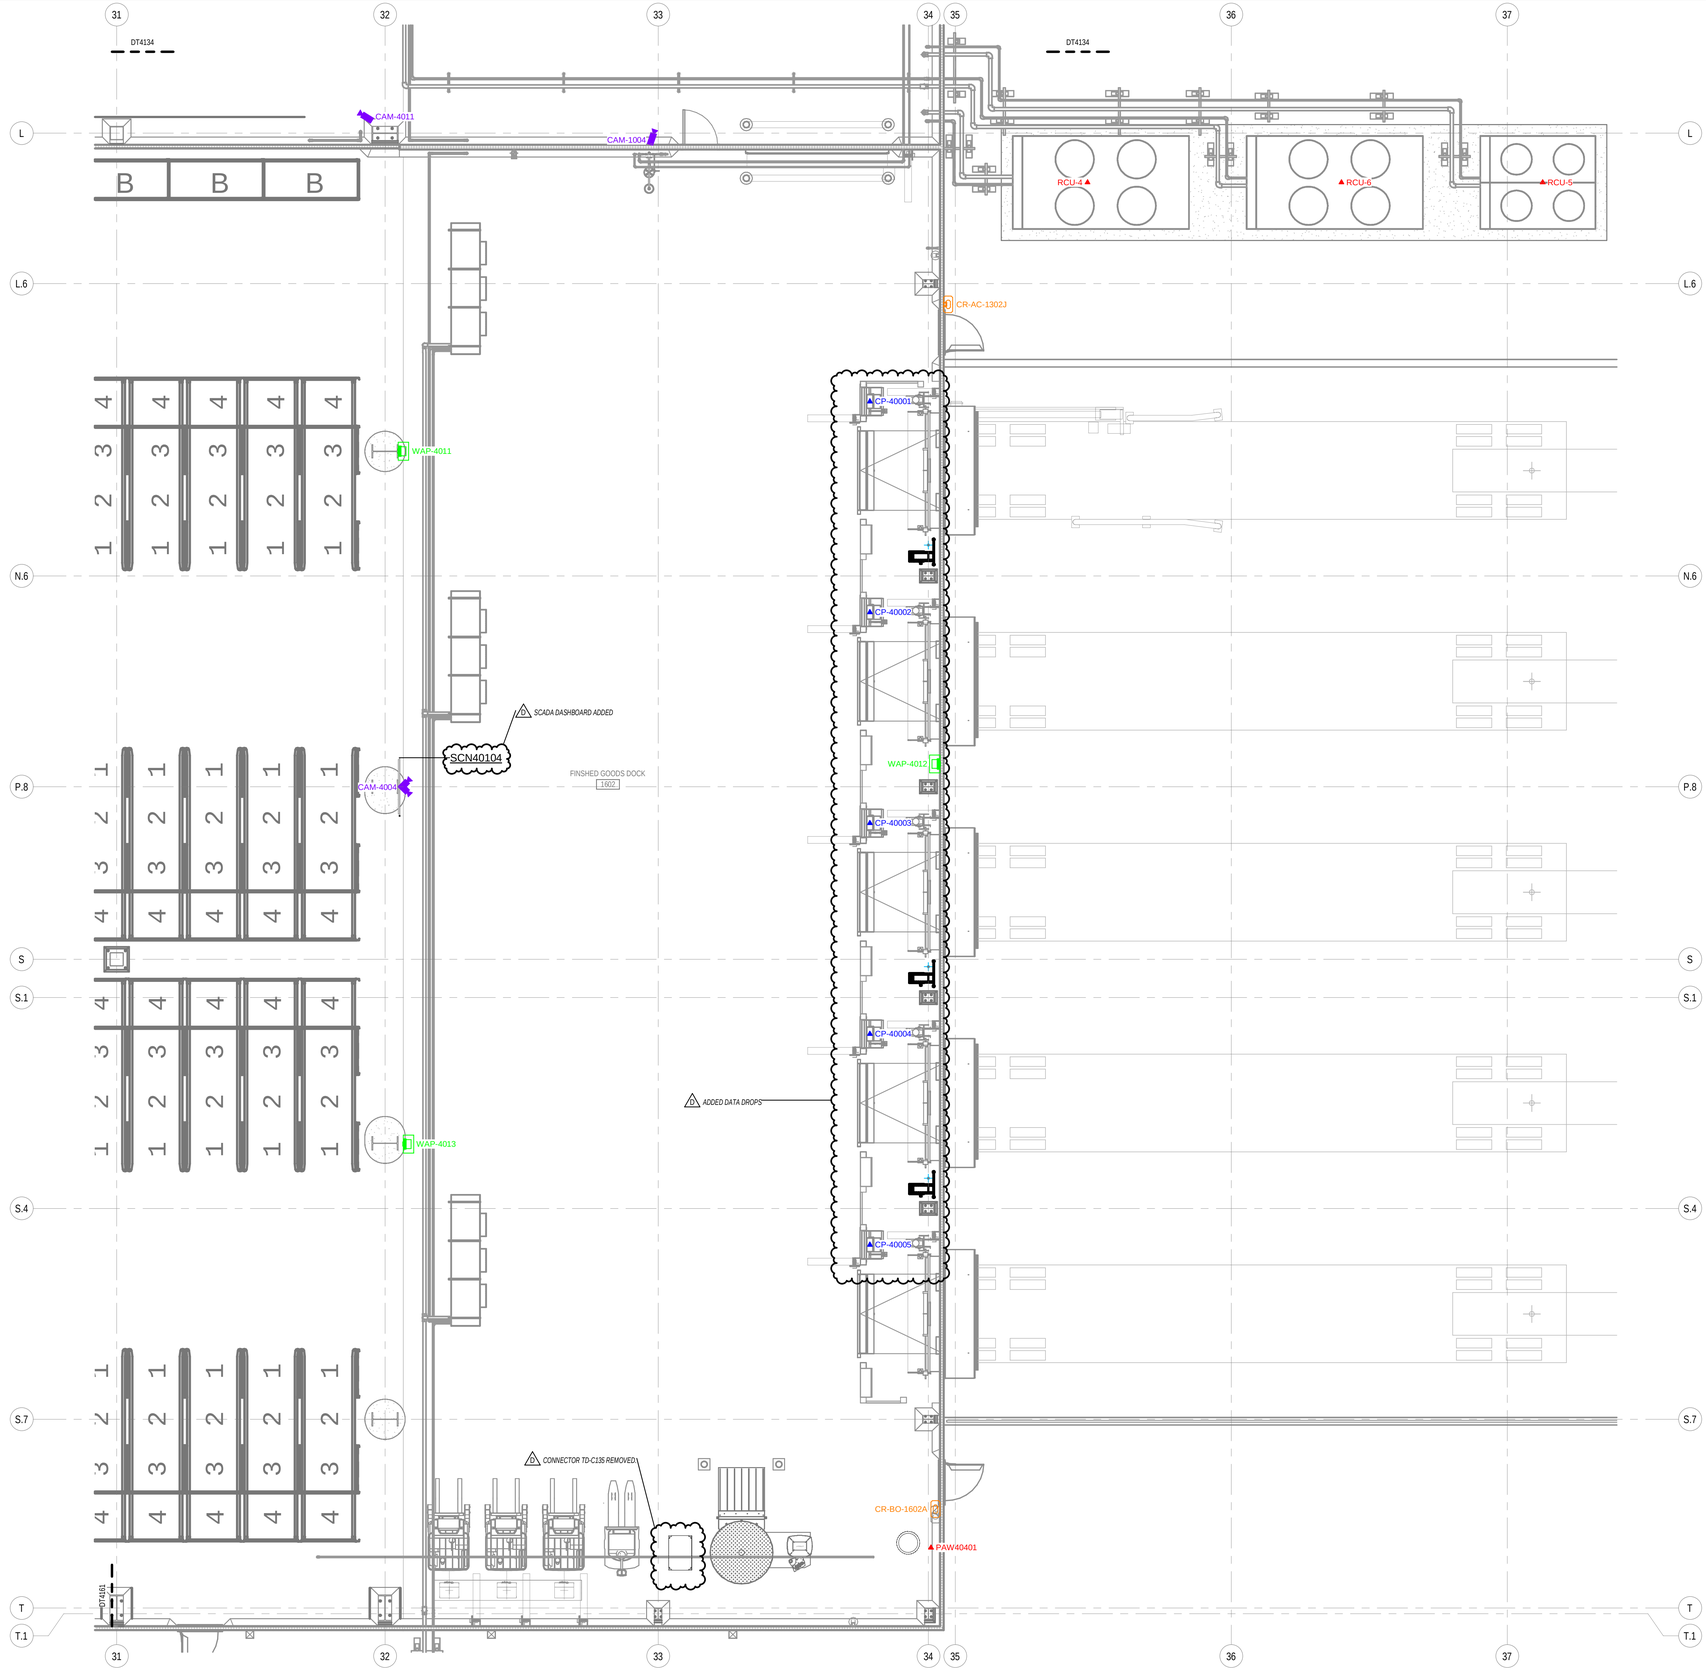

A1 ENLARGED PROCESS TELECOM 1ST FLOOR PLAN, AREA 6 SECTOR 2

SCALE: 3/16" = 1'-0"

0' 4' 8' 12' 16'

TELECOMM / DATA CONNECTION SCHEDULE

EQUIPMENT ID	EQUIPMENT DESCRIPTION	IDF	SWITCH / PORT
CAM-4011	CAMERA	2I05	2I05CS-SW01_5
WAP-4011	WIRELESS ACCESS POINT	2I05	2I05IT-SW01_11
CAM-1004	CAMERA	2I06	2I06CS-SW01_9
CAM-4004	DUAL CAMERA	2I06	2I06CS-SW01_12
CP-40001	DOCK LEVELER CONTROL PANEL - FINISHED GOODS DOCK 1602F	2I06	2I06IT-SW01_16
CP-40002	DOCK LEVELER CONTROL PANEL - FINISHED GOODS DOCK 1602E	2I06	2I06IT-SW01_17
CP-40003	DOCK LEVELER CONTROL PANEL - FINISHED GOODS DOCK 1602D	2I06	2I06IT-SW01_18
CP-40004	DOCK LEVELER CONTROL PANEL - FINISHED GOODS DOCK 1602C	2I06	2I06IT-SW01_19
CP-40005	DOCK LEVELER CONTROL PANEL - FINISHED GOODS DOCK 1602B	2I06	2I06IT-SW01_20
PAW40401	PALLET WRAPPER	2I06	2I06OT-SW01_3
RCU-4	REFRIGERATION CONDENSING UNIT #4	2I06	2I06OT-SW01_10
RCU-5	REFRIGERATION CONDENSING UNIT #5	2I06	2I06OT-SW01_9
RCU-6	REFRIGERATION CONDENSING UNIT #6 - NEST RUN DOCK	2I06	2I06OT-SW01_11
SCN40104	SCADA DASHBOARD	2I06	2I06OT-SW01_16
WAP-4012	WIRELESS ACCESS POINT	2I06	2I06IT-SW01_6
WAP-4013	WIRELESS ACCESS POINT	2I06	2I06IT-SW01_7

Grand total: 16

ACCESS CONTROL CONNECTION SCHEDULE

EQUIPMENT ID	EQUIPMENT DESCRIPTION	FED FROM
CR-AC-1302J	CARD READER	ACP-1001_4
CR-BO-1602A	EMPLOYEE BADGE OUT	ACP-1001_5

Grand total: 2

NOTES

1. ALL NETWORK DROPS SHALL BE TAGGED ON BOTH ENDS OF CABLE WITH "FROM / TO" FORMAT WITH BRADY B-427 ROTATING VINYL WIRE LABELS. (EX. 2I01IT-SW01_24 / TD-1001)

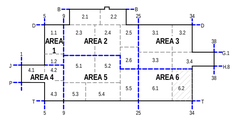

KEY PLAN

SECTORS

N

OWNER

PROJECT INFORMATION

VITAL FARMS
EGG CENTRAL 2
SEYMOUR,IN

OPERATING AS:
THE STELLAR GROUP
2900 HARTLEY ROAD, JACKSONVILLE, FL, 32257 (904) 260-2900
WWW.STELLAR.NET

SEAL

Professional certification. I hereby certify that these documents were prepared or approved by me, and that I am a duly licensed professional architect/engineer under the laws of the state of IN.

CONSULTANT

The Stellar Group, Inc.
All rights reserved. No part of this work may be used, reproduced, distributed, displayed, or otherwise communicated in any form or by any means without the prior written consent of The Stellar Group, Inc.

REVISIONS

NO.	DESCRIPTION	DATE
A	DESIGN DEVELOPMENT 2	12/12/2025
B	ISSUED FOR BID	01/16/2026
C	REVISED FOR BID	02/06/2026
D	GMP ISSUE	04/02/2026

DATE ISSUED:	12/12/2025
DESIGNED BY:	EJT
REVIEWED BY:	MAM
A/E/OR:	
PROJECT NUMBER:	07645

SHEET TITLE

PROCESS TELECOM 1ST FLOOR PLAN, AREA 6 SECTOR 2

SHEET ID

DT4162

PRINT IN COLOR

4/3/2026 1:15:05 AM Autodesk Docs://07645_Vital Farms Egg Central Station 2/07645_VF EGG ST'A 2_D_R23.rvt