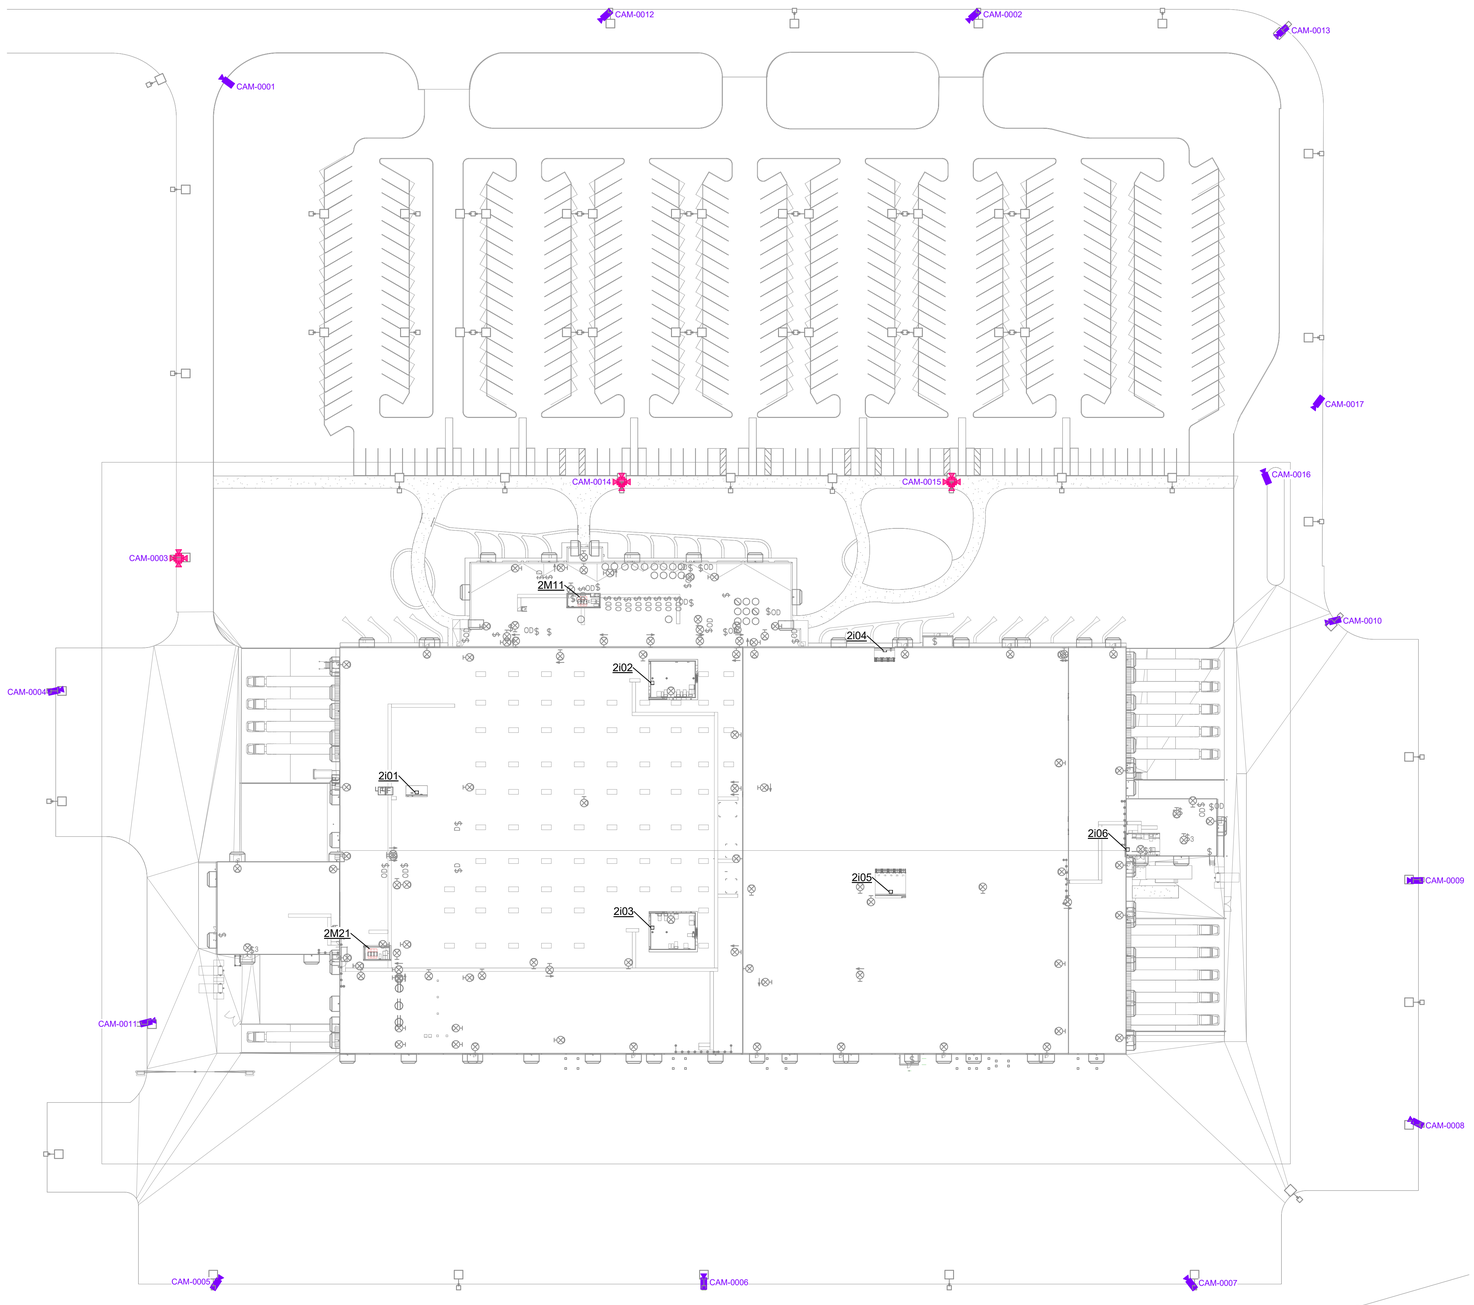

A1 OVERALL SITE CAMERA LOCATIONS

SCALE: 1" = 50'-0"

0' 15' 30' 60' 90'

TELECOMM / DATA CONNECTION SCHEDULE

EQUIPMENT ID	EQUIPMENT DESCRIPTION	IDF	SWITCH / PORT
CAM-0007	CAMERA	2I06	2I06CS-SW01_1
CAM-0008	CAMERA	2I06	2I06CS-SW01_2
CAM-0009	CAMERA	2I06	2I06CS-SW01_3
CAM-0010	CAMERA	2I06	2I06CS-SW01_4
CAM-0013	CAMERA	2I06	2I06CS-SW01_5
CAM-0016	CAMERA	2I06	2I06CS-SW01_6
CAM-0017	CAMERA	2I06	2I06CS-SW01_7
CAM-0001	CAMERA	2M11	2M11CS-SW01_1
CAM-0002	CAMERA	2M11	2M11CS-SW01_2
CAM-0003	QUAD CAMERA	2M11	2M11CS-SW01_3
CAM-0012	CAMERA	2M11	2M11CS-SW01_7
CAM-0014	QUAD CAMERA	2M11	2M11CS-SW01_8
CAM-0015	QUAD CAMERA	2M11	2M11CS-SW01_9
CAM-0004	CAMERA	2M21	2M21CS-SW01_1
CAM-0005	CAMERA	2M21	2M21CS-SW01_2
CAM-0006	CAMERA	2M21	2M21CS-SW01_3
CAM-0011	CAMERA	2M21	2M21CS-SW01_4

Grand total: 17

NOTES

1. ALL NETWORK DROPS SHALL BE TAGGED ON BOTH ENDS OF CABLE WITH "FROM / TO" FORMAT WITH BRADY B-427 ROTATING VINYL WIRE LABELS. (EX. 2I01IT-SW01_24 / TD-1001)

KEY PLAN

SECTORS

N

OWNER

PROJECT INFORMATION

VITAL FARMS
EGG CENTRAL 2
SEYMOUR,IN

stellar
TAKING SOLUTIONS FURTHER

OPERATING AS:
THE STELLAR GROUP
2900 HARTLEY ROAD, JACKSONVILLE, FL 32257 (904) 260-2900
WWW.STELLAR.NET

SEAL

Professional certification. I hereby certify that these documents were prepared or approved by me, and that I am a duly licensed professional architect/engineer under the laws of the state of IN

CONSULTANT

The Stellar Group, Inc.
All rights reserved. No part of this work may be used, reproduced, distributed, displayed, or otherwise communicated in any form or by any means without the prior written consent of The Stellar Group, Inc.

REVISIONS

NO.	DESCRIPTION	DATE
A	DESIGN DEVELOPMENT 2	12/12/2025
B	ISSUED FOR BID	01/16/2026
C	REVISED FOR BID	02/06/2026

DATE ISSUED:	12/12/2025
DESIGNED BY:	ARS
REVIEWED BY:	CDS
A/E/OR:	
PROJECT NUMBER:	07645

SHEET TITLE

PROCESS TELECOM OVERALL SITE CAMERA LOCATIONS

SHEET ID

DT1011

PRINT IN COLOR

2/6/2026 3:33:38 PM Autodesk Docs://07645_Vital Farms Egg Central Station 2/07645_VF EGG STA 2_D_R23.rvt