TELECOMM / DATA CONNECTION SCHEDULE

EQUIPMENT ID	EQUIPMENT DESCRIPTION	IDF	SWITCH / PORT
CAM-3001	CAMERA	2I01	2I01IT-SW01_1
CAM-4008	CAMERA	2I03	2I03CS-SW01_10
CAM-4012	CAMERA	2I03	2I03CS-SW01_11
CAM-3005	CAMERA	2M21	2M21CS-SW01_8
CAM-4006	CAMERA	2M21	2M21CS-SW01_11
CAM-4007	CAMERA	2M21	2M21CS-SW01_12
CAM-4013	CAMERA	2M21	2M21CS-SW01_13

Grand total: 7

NOTES

1. ALL NETWORK DROPS SHALL BE TAGGED ON BOTH ENDS OF CABLE WITH "FROM / TO" FORMAT WITH BRADY B-427 ROTATING VINYL WIRE LABELS. (EX. 2I01IT-SW01_24 / TD-1001)

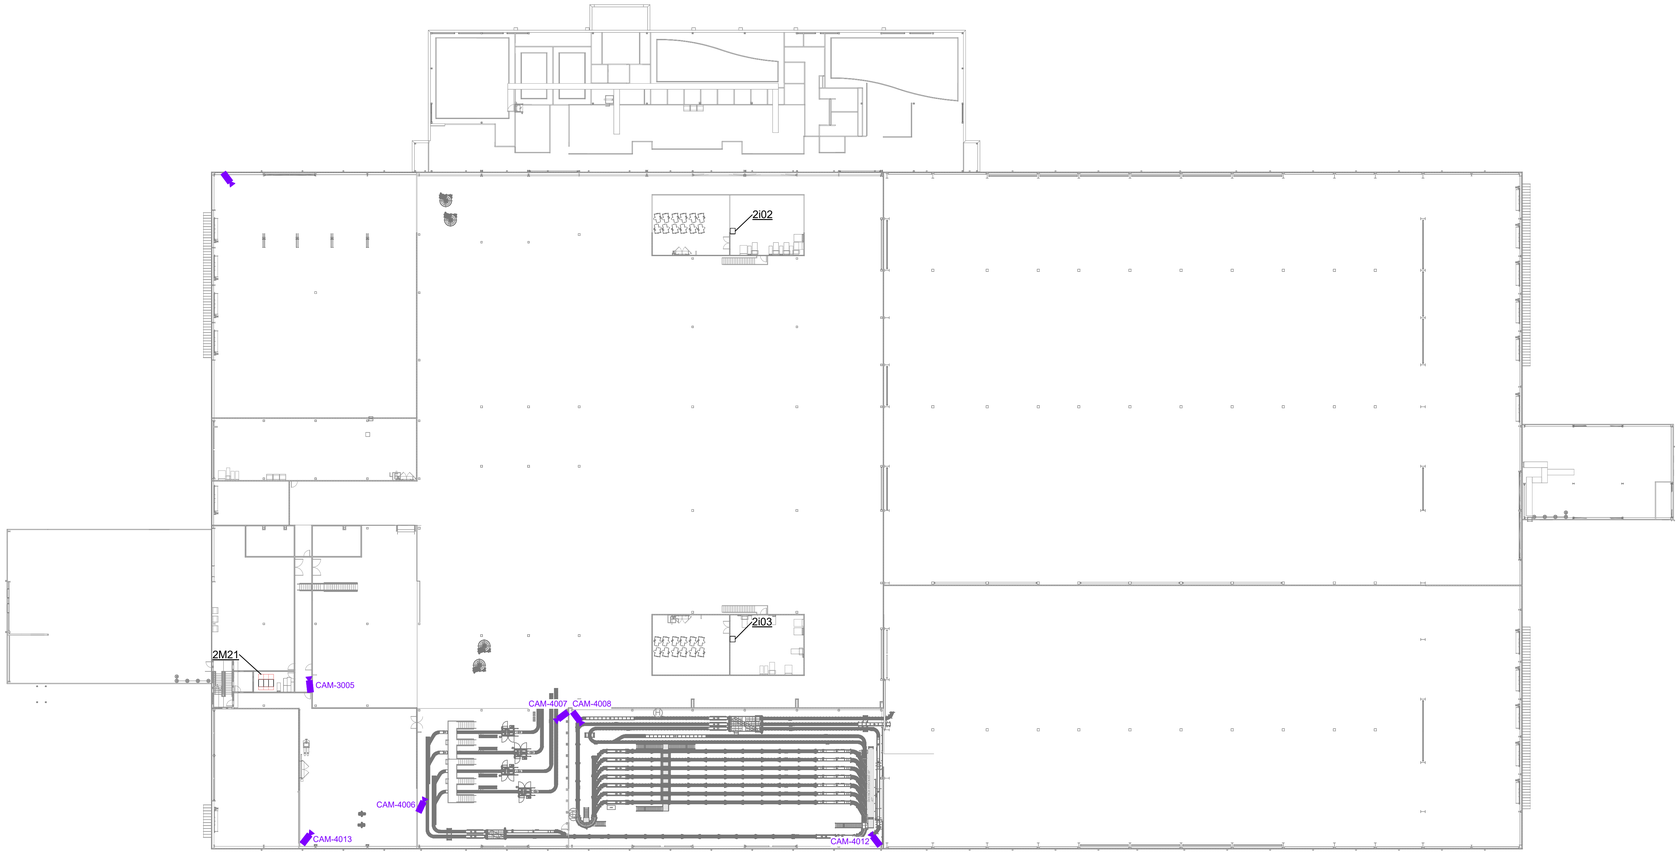

A1 OVERALL 2ND FLOOR CAMERA LOCATIONS

SCALE: 1" = 30'-0"

0' 15' 30' 60' 90'

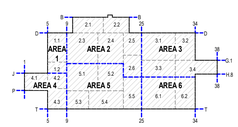

KEY PLAN

SECTORS

N

OWNER

PROJECT INFORMATION

VITAL FARMS
EGG CENTRAL 2
SEYMOUR,IN

stellar
TAKING SOLUTIONS FURTHER

OPERATING AS:
THE STELLAR GROUP
2900 HARTLEY ROAD, JACKSONVILLE, FL 32257 (904) 260-2900
WWW.STELLAR.NET

SEAL

Professional certification. I hereby certify that these documents were prepared or approved by me, and that I am a duly licensed professional architect/engineer under the laws of the state of IN

CONSULTANT

The Stellar Group, Inc.
All rights reserved. No part of this work may be used, reproduced, distributed, displayed, or otherwise communicated in any form or by any means without the prior written consent of The Stellar Group, Inc.

REVISIONS

NO.	DESCRIPTION	DATE
A	DESIGN DEVELOPMENT 2	12/12/2025
B	ISSUED FOR BID	01/16/2026
C	REVISED FOR BID	02/06/2026

DATE ISSUED:	12/12/2025
DESIGNED BY:	ARS
REVIEWED BY:	CDS
A/EOR:	
PROJECT NUMBER:	07645

SHEET TITLE

PROCESS TELECOM OVERALL 2ND FLOOR CAMERA LOCATIONS

SHEET ID

DT1211

PRINT IN COLOR

2/6/2026 3:30:49 PM Autodesk Docs://07645_Vital Farms Egg Central Station 2/07645_VF EGG STA 2_D_R23.rvt