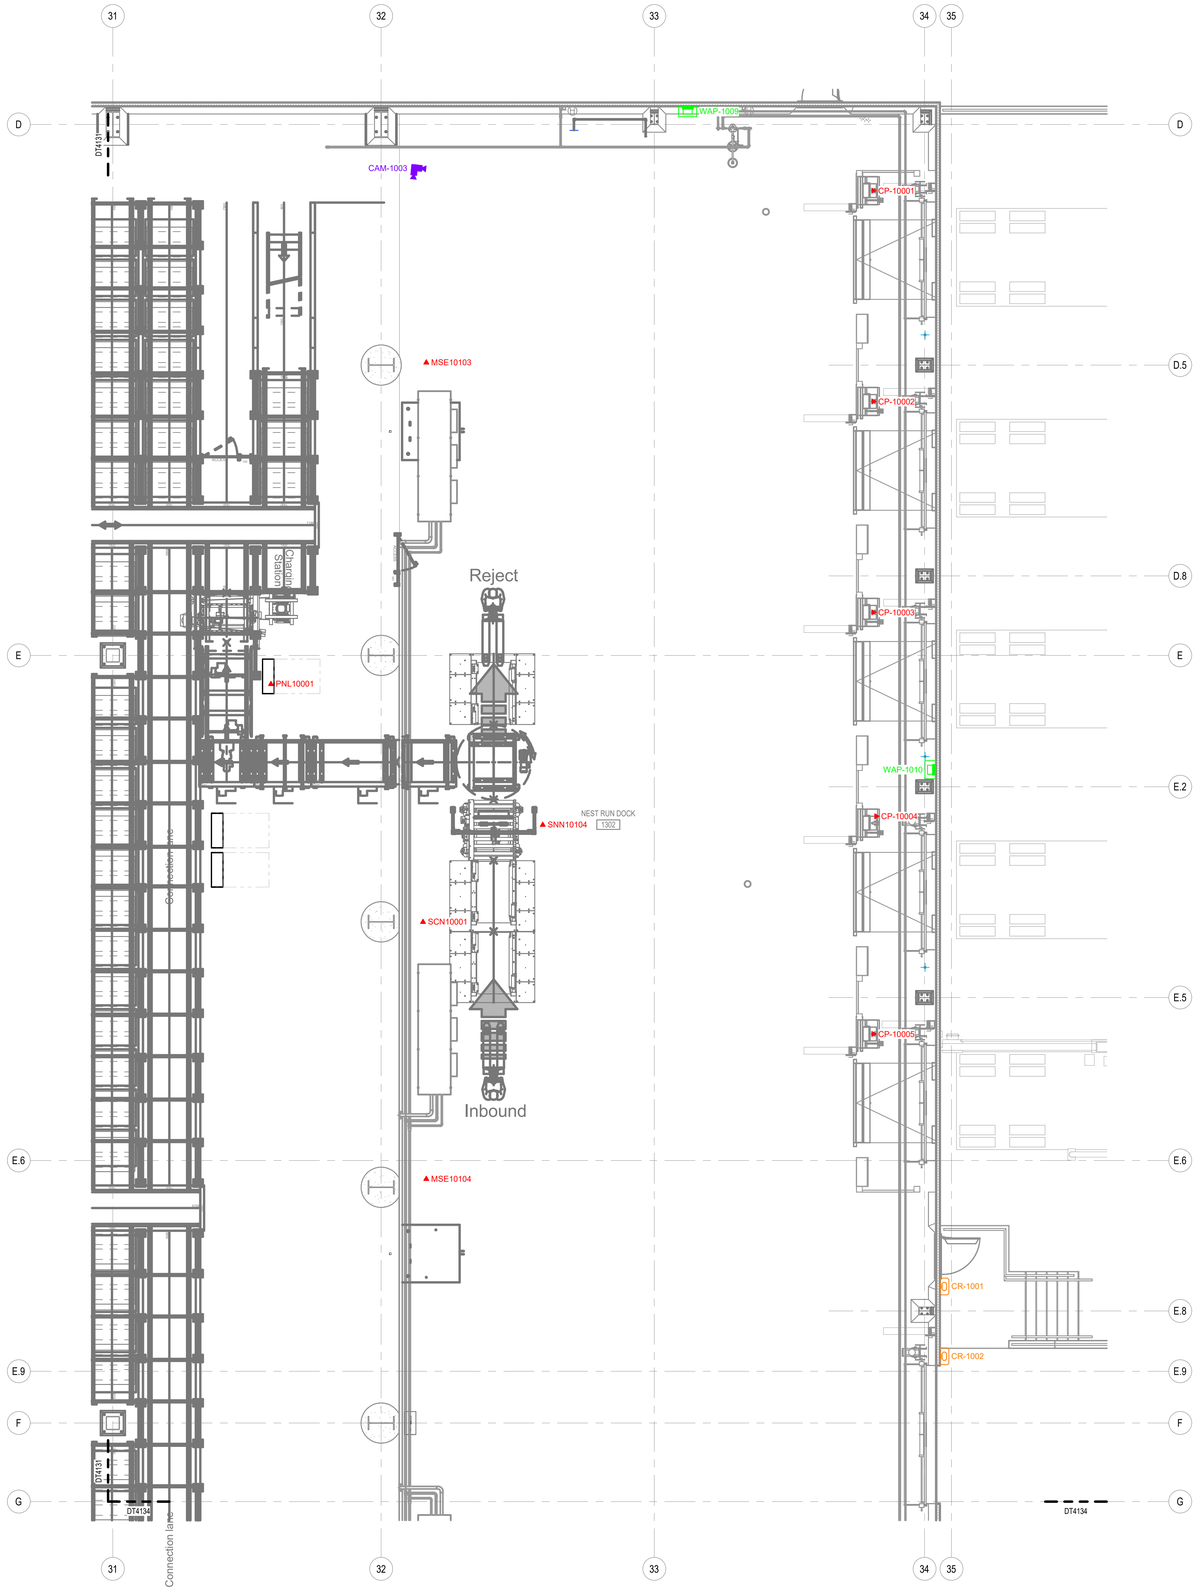

A1 ENLARGED PROCESS TELECOM 1ST FLOOR PLAN, AREA 3 SECTOR 2

SCALE: 3/16" = 1'-0"

0' 4' 8' 12' 16'

TELECOMM / DATA CONNECTION SCHEDULE

EQUIPMENT ID	EQUIPMENT DESCRIPTION	IDF	SWITCH / PORT
MSE10103	OVOTRACK PC STATION WITH PRINTER	204	204OT-SW01_3
PNL10001	VERTICAL CONVEYOR PANEL	204	204OT-SW01_1
SCN10001	OVOTRACK TV	204	204OT-SW01_4
CAM-1003	DUAL CAMERA	206	206CS-SW01_8
CP-10001	DOCK LEVELER CONTROL PANEL - RECEIVING DOCK 1302B	206	206OT-SW01_5
CP-10002	DOCK LEVELER CONTROL PANEL - RECEIVING DOCK 1302C	206	206OT-SW01_6
CP-10003	DOCK LEVELER CONTROL PANEL - RECEIVING DOCK 1302D	206	206OT-SW01_7
CP-10004	DOCK LEVELER CONTROL PANEL - RECEIVING DOCK 1302E	206	206OT-SW01_8
CP-10005	DOCK LEVELER CONTROL PANEL - RECEIVING DOCK 1302F	206	206OT-SW01_9
MSE10104	OVOTRACK PC STATION WITH PRINTER	206	206OT-SW01_1
SNN10104	OVOTRACK WEIGHSCALE SCAN STATION	206	206OT-SW01_2
WAP-1009	WIRELESS ACCESS POINT	206	206IT-SW01_1
WAP-1010	WIRELESS ACCESS POINT	206	206IT-SW01_2

Grand total: 13

ACCESS CONTROL CONNECTION SCHEDULE

EQUIPMENT ID	EQUIPMENT DESCRIPTION	FED FROM
CR-1001	CARD READER	2ACP03_1
CR-1002	CARD READER	2ACP03_2

Grand total: 2

NOTES

1. ALL NETWORK DROPS SHALL BE TAGGED ON BOTH ENDS OF CABLE WITH "FROM / TO" FORMAT WITH BRADY B-427 ROTATING VINYL WIRE LABELS. (EX. 2I01IT-SW01_24 / TD-1001)

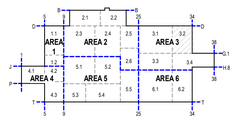

KEY PLAN

SECTORS

N

OWNER

PROJECT INFORMATION

VITAL FARMS
EGG CENTRAL 2
SEYMOUR,IN

stellar
TAKING SOLUTIONS FURTHER

OPERATING AS:
THE STELLAR GROUP
2900 HARTLEY ROAD, JACKSONVILLE, FL 32257 (904) 260-2900
WWW.STELLAR.NET

SEAL

Professional certification. I hereby certify that these documents were prepared or approved by me, and that I am a duly licensed professional architect/engineer under the laws of the state of IN.

CONSULTANT

The Stellar Group, Inc.
All rights reserved. No part of this work may be used, reproduced, distributed, displayed, or otherwise communicated in any form or by any means without the prior written consent of The Stellar Group, Inc.

REVISIONS

NO.	DESCRIPTION	DATE
A	DESIGN DEVELOPMENT 2	12/12/2025
B	ISSUED FOR BID	01/16/2026
C	REVISED FOR BID	02/06/2026

DATE ISSUED:	12/12/2025
DESIGNED BY:	EJT
REVIEWED BY:	MAM
A/EOR:	
PROJECT NUMBER:	076445

SHEET TITLE

PROCESS TELECOM 1ST FLOOR PLAN, AREA 3 SECTOR 2

SHEET ID

DT4132

PRINT IN COLOR

2/6/2026 3:17:29 PM Autodesk Docs://076445_Vital Farms Egg Central Station 2/076445_VF EGG STA 2_D_R23.rvt