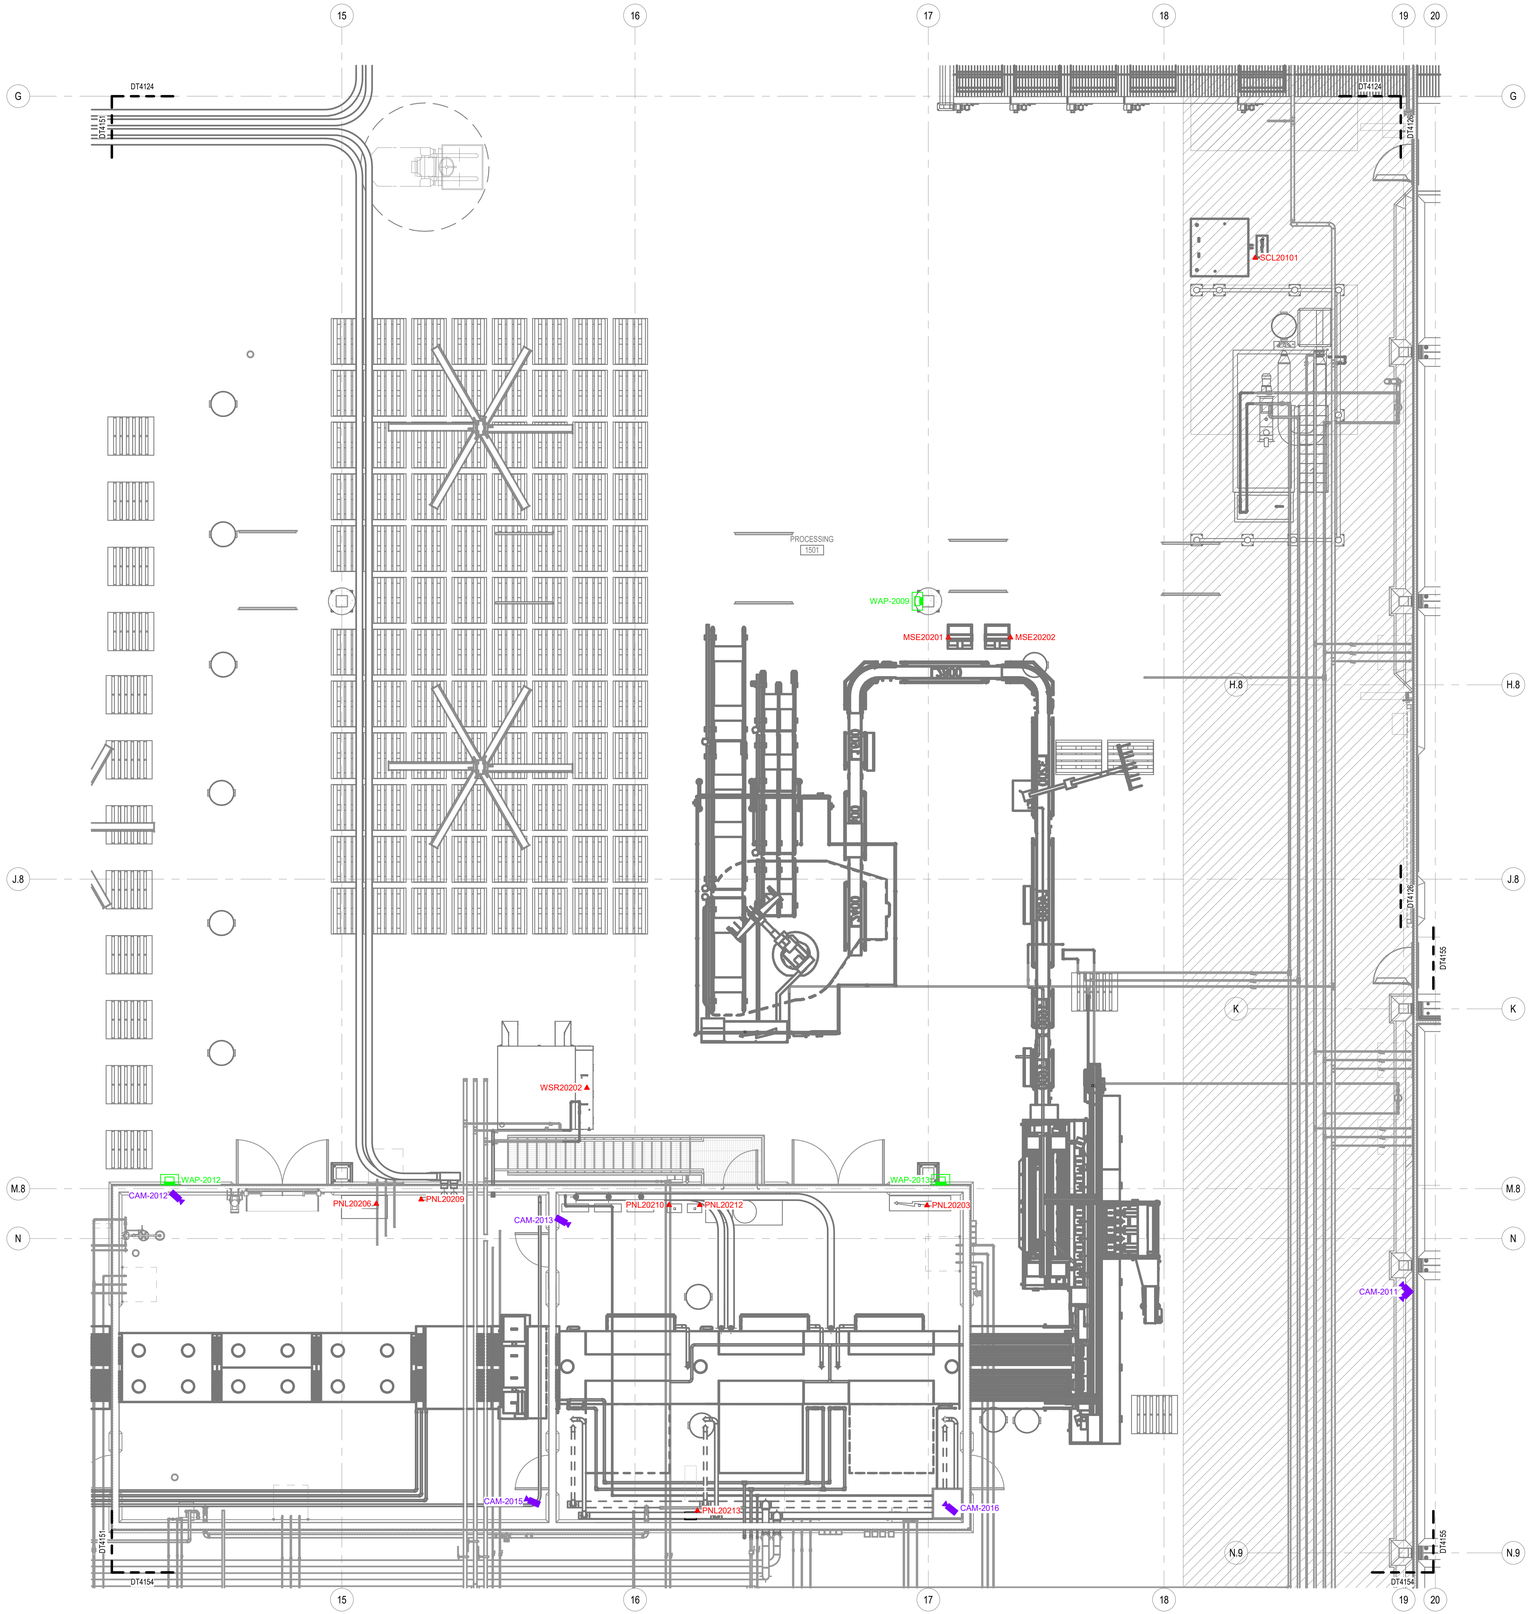

A1 ENLARGED PROCESS TELECOM 1ST FLOOR PLAN, AREA 5 SECTOR 2

SCALE: 3/16" = 1'-0"

0' 4' 8' 12' 16'

TELECOMM / DATA CONNECTION SCHEDULE

EQUIPMENT ID	EQUIPMENT DESCRIPTION	IDF	SWITCH / PORT
CAM-2011	DUAL CAMERA	203	203CS-SW01_3
CAM-2012	CAMERA	203	203CS-SW01_4
CAM-2013	CAMERA	203	203CS-SW01_5
CAM-2015	CAMERA	203	203CS-SW01_6
CAM-2016	CAMERA	203	203CS-SW01_7
MSE20201	OPERATOR STATION	203	2i03OT-SW01_20
MSE20202	OPERATOR STATION	203	2i03OT-SW01_21
PNL20203	EGG WASHER CONTROL PANEL	203	203OT-SW01_1
PNL20206	EGG DRYER CONTROL PANEL	203	203OT-SW01_4
PNL20209	WALCHEM I-9 CONTROLLER	203	203OT-SW01_6
PNL20210	EGG WASH DOSING CONTROL BOX	203	203OT-SW01_7
PNL20212	CIP DOSING CONTROL BOX	203	203OT-SW01_8
PNL20213	PROCESS DATA PANEL	203	203OT-SW01_9
SCL20101	FLOOR SCALE	203	2i03OT-SW01_34
WAP-2009	WIRELESS ACCESS POINT	203	203IT-SW01_2
WAP-2012	WIRELESS ACCESS POINT	203	203IT-SW01_5
WAP-2013	WIRELESS ACCESS POINT	203	203IT-SW01_6
WSR20202	PARTS WASHER	203	2i03OT-SW01_33

Grand total: 18

NOTES

1. ALL NETWORK DROPS SHALL BE TAGGED ON BOTH ENDS OF CABLE WITH "FROM / TO" FORMAT WITH BRADY B-427 ROTATING VINYL WIRE LABELS. (EX. 2011T-SW01_24 / TD-1001)

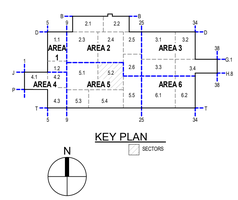

KEY PLAN

SECTORS

N

OWNER

EST. 2007 Vital FARMS®

PROJECT INFORMATION

VITAL FARMS
EGG CENTRAL 2
SEYMOUR,IN

stellar
TAKING SOLUTIONS FURTHER

OPERATING AS:
THE STELLAR GROUP
2900 HARTLEY ROAD, JACKSONVILLE, FL, 32257 (904) 260-2900
WWW.STELLAR.NET

SEAL

Professional certification. I hereby certify that these documents were prepared or approved by me, and that I am a duly licensed professional architect/engineer under the laws of the state of IN.

CONSULTANT

The Stellar Group, Inc.
All rights reserved. No part of this work may be used, reproduced, distributed, displayed, or otherwise communicated in any form or by any means without the prior written consent of The Stellar Group, Inc.

REVISIONS

NO.	DESCRIPTION	DATE
A	DESIGN DEVELOPMENT 2	12/12/2025
B	ISSUED FOR BID	01/16/2026
C	REVISED FOR BID	02/06/2026

DATE ISSUED:	12/12/2025
DESIGNED BY:	EJT
REVIEWED BY:	MAM
A/E/OR:	
PROJECT NUMBER:	07645

SHEET TITLE

PROCESS TELECOM 1ST FLOOR PLAN, AREA 5 SECTOR 2

SHEET ID

DT4152

PRINT IN COLOR

2/6/2026 3:20:12 PM Autodesk Docs://07645_Vital Farms Egg Central Station 2/07645_VF EGG STA 2_D_R23.rvt