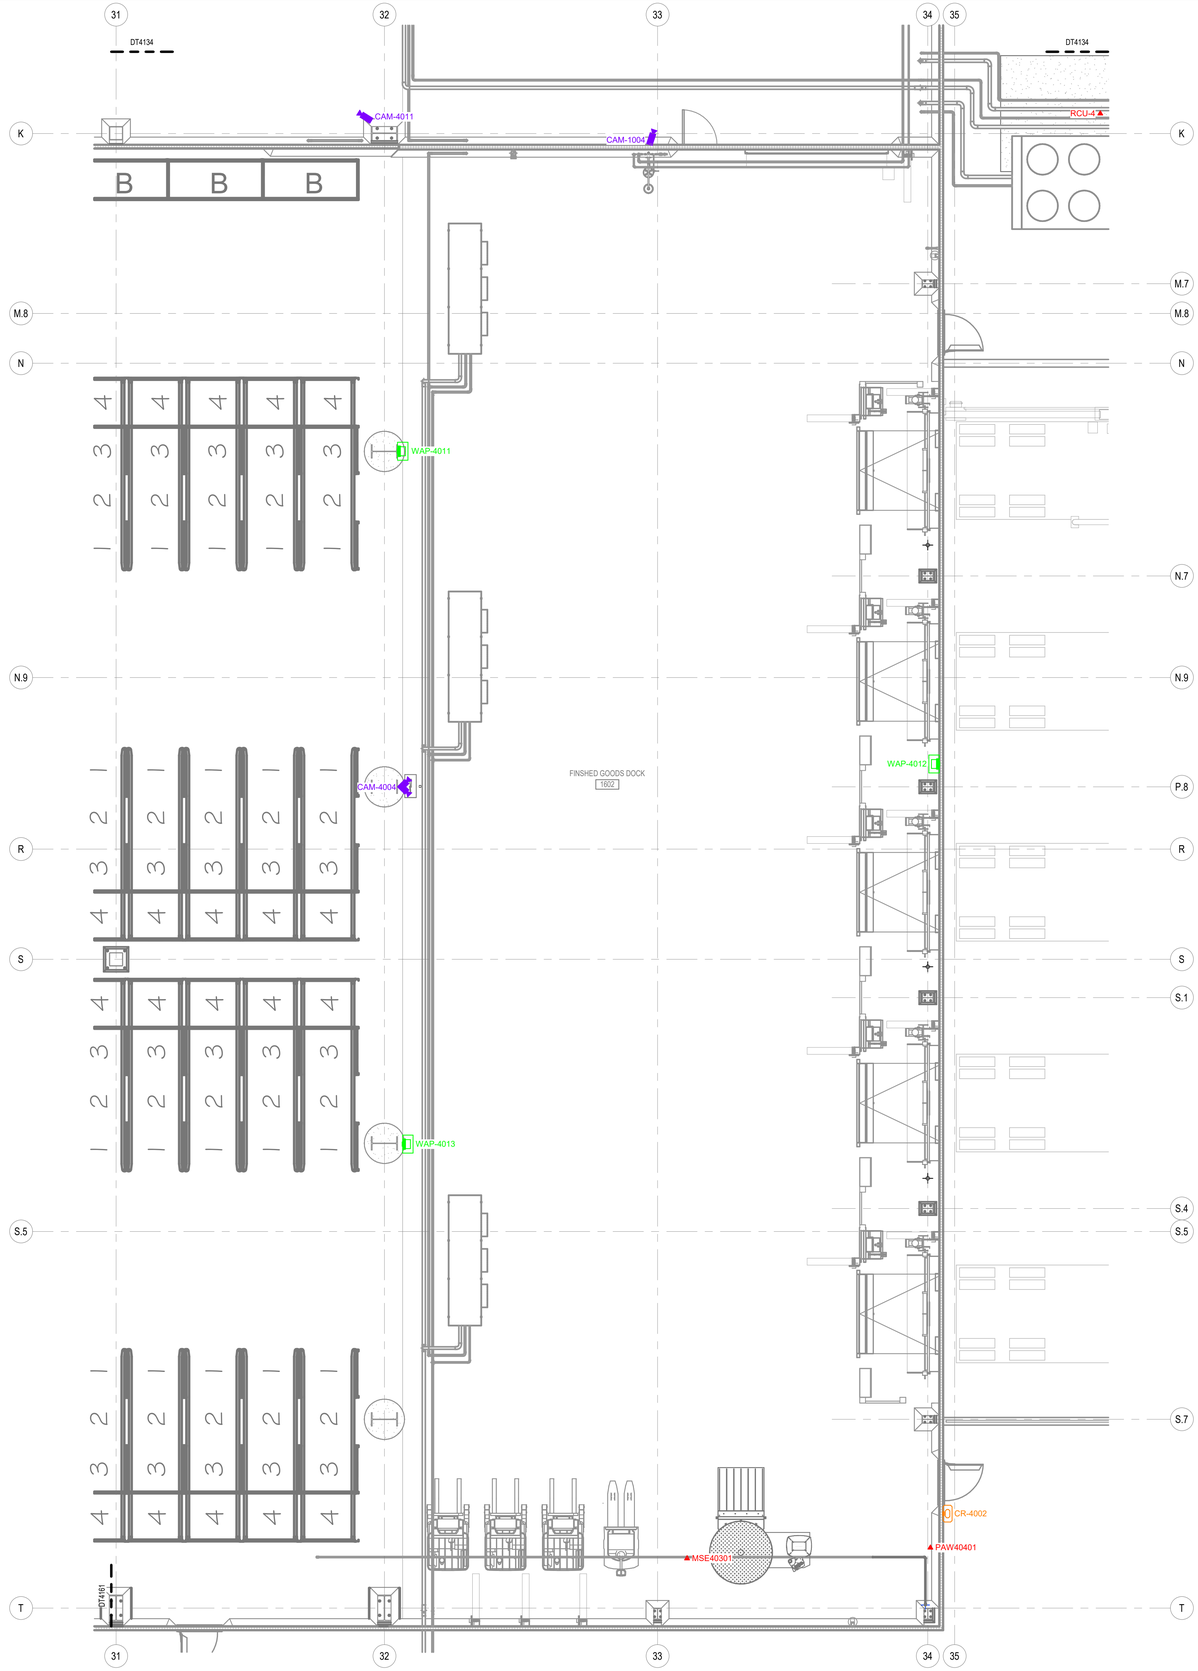

A1 ENLARGED PROCESS TELECOM 1ST FLOOR PLAN, AREA 6 SECTOR 2

SCALE: 3/16" = 1'-0"

0' 4' 8' 12' 16'

TELECOMM / DATA CONNECTION SCHEDULE

EQUIPMENT ID	EQUIPMENT DESCRIPTION	IDF	SWITCH / PORT
CAM-4011	CAMERA	205	205CS-SW01_5
MSE40301	OVOTRACK PC STATION WITH PRINTER	205	205OT-SW01_3
WAP-4011	WIRELESS ACCESS POINT	205	205IT-SW01_11
CAM-1004	CAMERA	206	206CS-SW01_9
CAM-4004	DUAL CAMERA	206	206CS-SW01_12
PAW40401	PALLET WRAPPER	206	206OT-SW01_3
RCU-4	REFRIGERATION CONDENSING UNIT #4	206	206OT-SW01_12
WAP-4012	WIRELESS ACCESS POINT	206	206IT-SW01_6
WAP-4013	WIRELESS ACCESS POINT	206	206IT-SW01_7

Grand total: 9

ACCESS CONTROL CONNECTION SCHEDULE

EQUIPMENT ID	EQUIPMENT DESCRIPTION	FED FROM
CR-4002	CARD READER	2ACP03_5

Grand total: 1

NOTES

1. ALL NETWORK DROPS SHALL BE TAGGED ON BOTH ENDS OF CABLE WITH "FROM / TO" FORMAT WITH BRADY B-427 ROTATING VINYL WIRE LABELS. (EX. 205IT-SW01_24 / TD-1001)

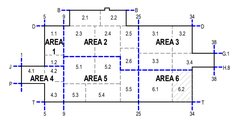

KEY PLAN

SECTORS

N

OWNER

PROJECT INFORMATION

VITAL FARMS
EGG CENTRAL 2
SEYMOUR,IN

stellar
TAKING SOLUTIONS FURTHER

OPERATING AS:
THE STELLAR GROUP
2900 HARTLEY ROAD, JACKSONVILLE, FL 32257 (904) 260-2900
WWW.STELLAR.NET

SEAL

Professional certification. I hereby certify that these documents were prepared or approved by me, and that I am a duly licensed professional architect/engineer under the laws of the state of IN.

CONSULTANT

The Stellar Group, Inc.
All rights reserved. No part of this work may be used, reproduced, distributed, displayed, or otherwise communicated in any form or by any means without the prior written consent of The Stellar Group, Inc.

REVISIONS

NO.	DESCRIPTION	DATE
A	DESIGN DEVELOPMENT 2	12/12/2025
B	ISSUED FOR BID	01/16/2026
C	REVISED FOR BID	02/06/2026

DATE ISSUED:	12/12/2025
DESIGNED BY:	EJT
REVIEWED BY:	MAM
A/E/OR:	
PROJECT NUMBER:	07645

SHEET TITLE

PROCESS TELECOM 1ST FLOOR PLAN, AREA 6 SECTOR 2

SHEET ID

DT4162

PRINT IN COLOR

2/6/2026 3:21:52 PM Autodesk Docs://07645_Vital Farms Egg Central Station 2/07645_VF EGG STA 2_D_R23.rvt