TELECOMM / DATA CONNECTION SCHEDULE

EQUIPMENT ID	EQUIPMENT DESCRIPTION	IDF	SWITCH / PORT
AHU-1	AIR HANDLING UNIT #1	2M21	2M21OT-SW02_1
AHU-2	AIR HANDLING UNIT #2	2M21	2M21OT-SW02_2
AHU-3	AIR HANDLING UNIT #3	2M21	2M21OT-SW02_3
CAM-3005	CAMERA	2M21	2M21CS-SW01_8
CRAC-2	SPLIT SYSTEM AIR HANDLING UNIT - MDF RM	2M21	2M21OT-SW02_6
ERV-1	ENERGY RECOVERY UNIT #1	2M21	2M21OT-SW02_7
TD-3011	RJ45 DATA JACK	2M21	2M21IT-SW01_26
TD-3012	RJ45 DATA JACK	2M21	2M21IT-SW01_27
TD-3013	RJ45 DATA JACK	2M21	2M21IT-SW01_28
TD-3014	RJ45 DATA JACK	2M21	2M21IT-SW01_29
TD-3015	RJ45 DATA JACK	2M21	2M21IT-SW01_30
TD-3016	RJ45 DATA JACK	2M21	2M21IT-SW01_31
TD-3017	RJ45 DATA JACK	2M21	2M21IT-SW01_32
TD-3018	RJ45 DATA JACK	2M21	2M21IT-SW01_33
TD-3019	PARTS STORAGE LAPTOP	2M21	2M21IT-SW01_34
TD-3020	PARTS STORAGE PRINTER	2M21	2M21IT-SW01_35
TD-3021	RJ45 DATA JACK	2M21	2M21IT-SW01_36
TD-3022	RJ45 DATA JACK	2M21	2M21IT-SW01_37
WAP-3008	WIRELESS ACCESS POINT	2M21	2M21IT-SW01_3
WAP-3009	WIRELESS ACCESS POINT	2M21	2M21IT-SW01_4

Grand total: 20

ACCESS CONTROL CONNECTION SCHEDULE

EQUIPMENT ID	EQUIPMENT DESCRIPTION	FED FROM
CR-2004	CARD READER - IT ROOM	2ACP02_7

Grand total: 1

NOTES

1. ALL NETWORK DROPS SHALL BE TAGGED ON BOTH ENDS OF CABLE WITH "FROM / TO" FORMAT WITH BRADY B-427 ROTATING VINYL WIRE LABELS. (EX. 2611T-SW01_24 / TD-1001)

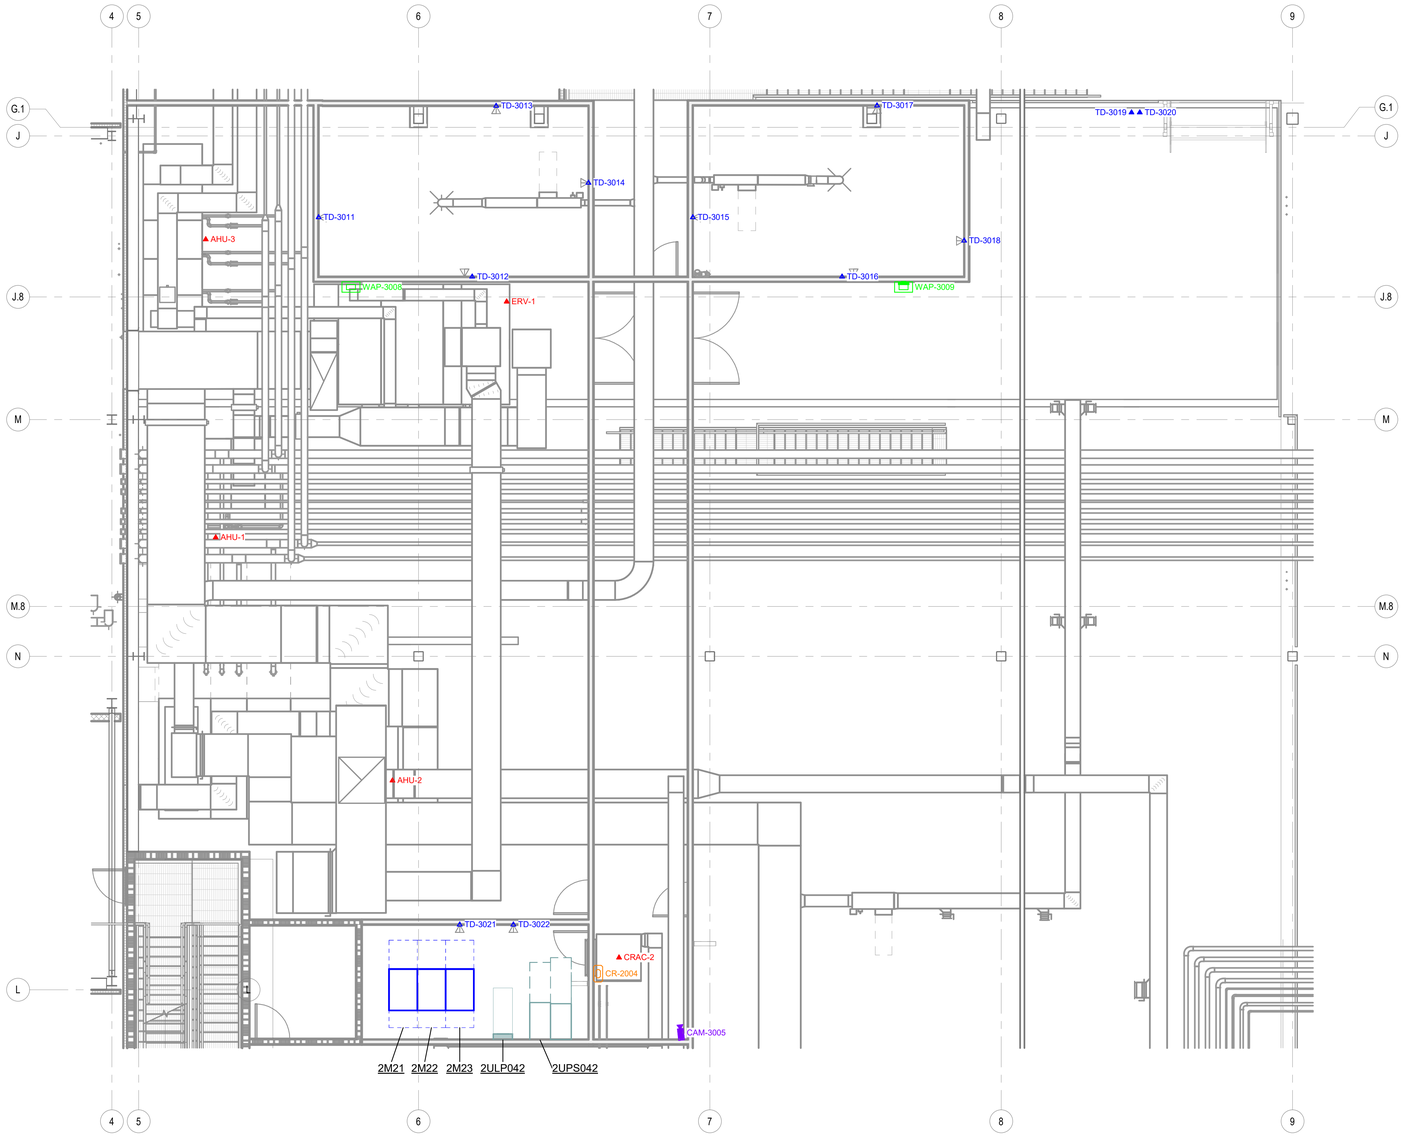

A1 ENLARGED PROCESS 2ND FLOOR PLAN AREA 4, SECTOR 2

SCALE: 3/16" = 1'-0"

0' 4' 8' 12' 16'

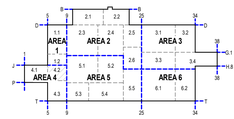

KEY PLAN

SECTORS

N

OWNER

PROJECT INFORMATION

VITAL FARMS
EGG CENTRAL 2
SEYMOUR,IN

stellar
TAKING SOLUTIONS FURTHER

OPERATING AS:
THE STELLAR GROUP
2900 HARTLEY ROAD, JACKSONVILLE, FL, 32257 (904) 260-2900
WWW.STELLAR.NET

SEAL

Professional certification. I hereby certify that these documents were prepared or approved by me, and that I am a duly licensed professional architect/engineer under the laws of the state of IN.

CONSULTANT

The Stellar Group, Inc.
All rights reserved. No part of this work may be used, reproduced, distributed, displayed, or otherwise communicated in any form or by any means without the prior written consent of The Stellar Group, Inc.

REVISIONS

NO.	DESCRIPTION	DATE
A	DESIGN DEVELOPMENT 2	12/12/2025
B	ISSUED FOR BID	01/16/2026
C	REVISED FOR BID	02/06/2026

DATE ISSUED:	12/12/2025
DESIGNED BY:	EJT
REVIEWED BY:	MAM
A/E/OR:	
PROJECT NUMBER:	07645

SHEET TITLE

PROCESS TELECOM 2ND FLOOR PLAN, AREA 4 SECTOR 2

SHEET ID

DT4242

PRINT IN COLOR

2/7/2026 1:17:49 AM Autodesk Docs://07645_Vital Farms Egg Central Station 2/07645_VF EGG STA 2_D_R23.rvt